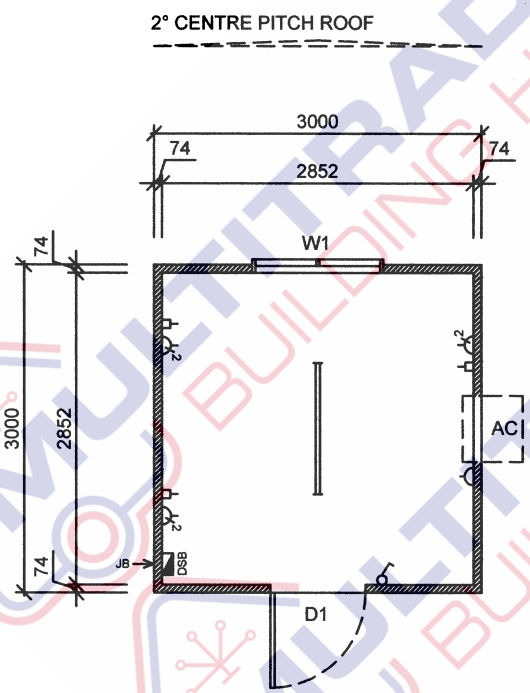

3.0x3.0m Office - Floor Plan

Scale 1:50

Colour Schedule

External

Cladding	-	Surfmist
Roof	-	Zincalume
Flashings	-	Surfmist
Capping	-	Surfmist
Door	-	Surfmist
Window	-	White

Internal

Vinyl	-	Grey
Walls	-	Grey
Ceiling	-	Mirage Pearl

Item List

Item	Qty	Description
D1	x(1)	2040x850mm External Metal Clad Door
W1	x(1)	900x1200mm Sliding Glass Window - Grey Glass
AC	x(1)	Frame & Cutout Only - For Wall Mounted Air Conditioner (Cutout Size - 605mm Wide x 385mm High)

Notes

- Built to Multitrade Building Hire Specification
- 2400mm Internal Ceiling Height

Electrical Legend

Icon	Qty	Description
DSB	x(1)	Distribution Switchboard
JB	x(1)	Junction Box - Electrical Point Of Entry
	x(1)	Light Switch
	x(1)	10amp Single GPO
2	x(3)	10amp Double GPO
	x(3)	Draw Wire With Blank Plate
	x(1)	36 Watt Double Fluorescent Light

CLIENT APPROVAL

Signature: Date:

Rev.	Description	Date	By
A	Issued for Approval	24/01/11	B1

MULTITRADE
BUILDING HIRE
TRANSPORTABLES

MULTITRADE
6 SOUTH TREES DRIVE
PO BOX 8005
SOUTH GLADSTONE
4680, QLD, AUSTRALIA

Phone: 07 4979 2333
Fax: 07 4979 1698
Email: multitrade@hotkey.net.au

www.multitrade.com.au

THIS DRAWING AND DESIGN IS THE SOLE PROPERTY OF HALBIMBU PTY LTD T/A MULTITRADE A.B.N. 40 033 426 884 IT MAY NOT BE REPRODUCED, COPIED WHOLE OR IN PART WITHOUT WRITTEN AUTHORITY.

CLIENT		DATE
		24/01/11
TITLE		SCALE
3.0x3.0m OFFICE		1:50
DESIGN WIND LOAD	DRAWN	CHECKED
C2 - CYCLONIC	B1	
DRAWING NUMBER	REVISION	SHEET SIZE
MBH-3030-OFF-01	A	A3