PRELIMINARY DRAWING

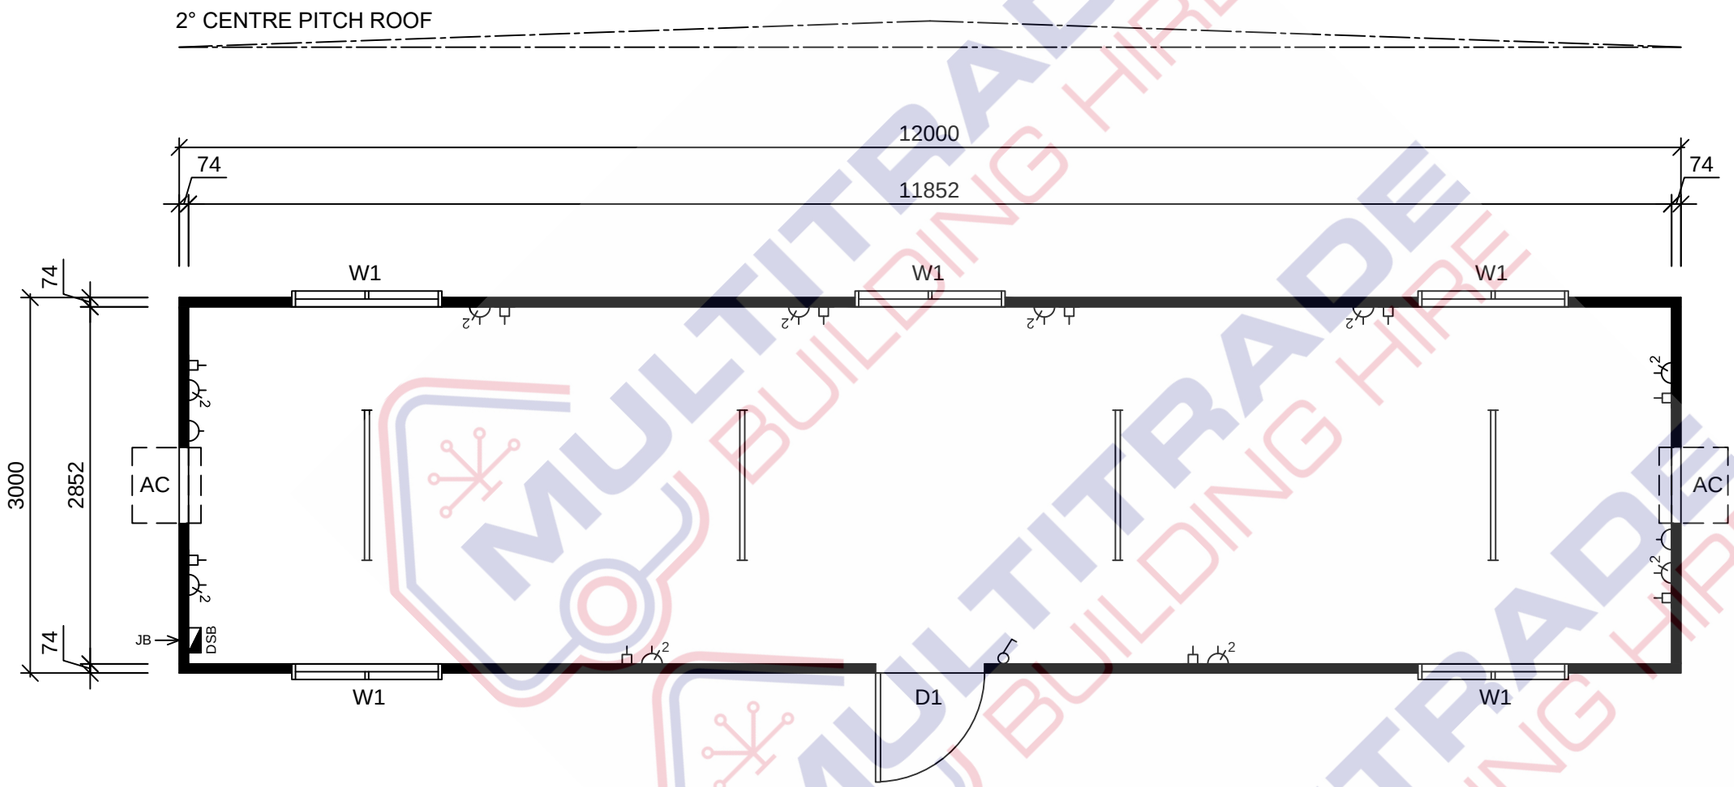

12.0x3.0m Office - Floor Plan

Scale 1:50

Colour Schedule

External		
Cladding	-	Surfmist
Roof	-	Zincalume
Capping	-	Surfmist
Gutter	-	Surfmist
Downpipe	-	Surfmist
Doors	-	White
Windows	-	White

Internal		
Vinyl	-	Grey
Walls	-	Grey
Ceiling	-	White
Cabinetry	-	White

Item List

Item	Qty	Description
D1	x(1)	2040x920mm External Metal Clad Door.
W1	x(5)	900x1200mm Sliding Glass Window - Grey Glass With Flyscreen.
AC	x(2)	Provision For Wall Mounted Air Conditioner Unit.

Notes

- Built To Multitrade Building Hire Specifications.
- 150x75mm PFC Chassis Bearers With C10015 Floor Joists @ 600mm Ctrs.
- 19mm T&G F11 Plywood Flooring.
- 2mm Commercial Vinyl Floor Covering.
- 2400mm Internal Ceiling Height.
- Horizontal 'Panelrib' Profile External Colorbond Cladding.
- Zincalume 'Trimdek' Profile Roof Sheeting.
- Pre-finished Plywood Internal Wall & Ceiling Lining With PVC Joiners , Cornice, Skirting & Corner Moulds.
- Wall & Ceiling Insulation.

Electrical Legend

Icon	Qty	Description
DSB	x(1)	Internal Distribution Switchboard
JB	x(1)	Junction Box - Electrical Point Of Entry
	x(1)	Light Switch
	x(2)	10amp Single GPO
	x(10)	10amp Double GPO
	x(10)	Draw Wire With Blank Plate
	x(4)	36 Watt Double Fluorescent Light

CLIENT APPROVAL

Signature: Date:

Rev.	Description	Date	By
A	Issued for Client Review	13/03/18	BW

MULTITRADE BUILDING HIRE

THIS DRAWING AND DESIGN IS THE SOLE PROPERTY OF JABEGIL PTY LTD T/A MULTITRADE BUILDING HIRE A.B.N. 36 010 138 600 IT MAY NOT BE REPRODUCED, COPIED WHOLE OR IN PART WITHOUT WRITTEN AUTHORITY.

CLIENT		DATE
		13/03/18
TITLE		SCALE
12.0x3.0m OFFICE		1:50
DESIGN WIND LOAD	DRAWN	CHECKED
C2 (W50C)	BW	
DRAWING NUMBER	REVISION	SHEET SIZE
SQF-3208-01	A	A3