PRELIMINARY DRAWING

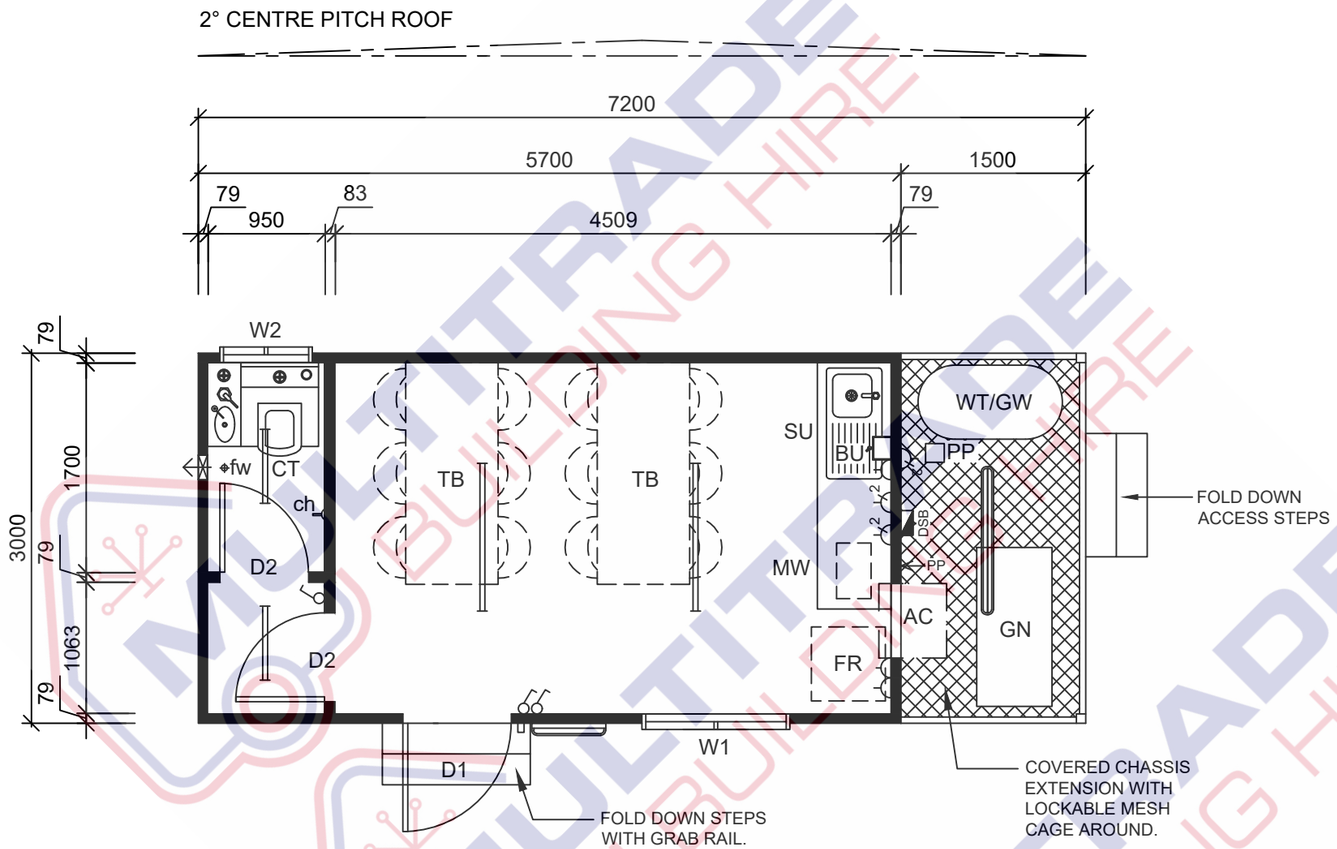

7.2x3.0m Site Crib Room/Toilet - Floor Plan

Scale 1:50

Colour Schedule

External		
Cladding	-	Surfmist
Roof	-	Zincalume
Capping	-	Surfmist
Doors	-	White
Windows	-	White

Internal		
Vinyl	-	Grey
Vinyl (R10)	-	Grey
Walls	-	Grey
Ceiling	-	White
Cabinetry	-	White

Item List

Item	Qty	Description
D1	x(1)	2040x920mm External Metal Clad Door With Passage Set, Hasp & Staple & Door Closer.
D2	x(2)	2040x720mm Internal Painted Hollow Core Door With Privacy Set & Door Closer.
W1	x(1)	1200x1200mm Sliding Glass Window - Grey Glass, With Full Cover Security Screen and Internal Roller Blind.
W2	x(1)	300x750mm Sliding Obscure Glass Window With Full Cover Security Screen.
AC	x(1)	2.7kw TECO Wall Mounted Reverse Cycle Air Conditioner.
GN	x(1)	6 kVa Kubota Lowboy Series 2 Mine Spec Single Phase Diesel Generator, Mounted On Covered Chassis Extension.
WT	x(1)	450 Ltr Potable Water Tank, On Metal Frame Over 'GW'.
GW	x(1)	450 Ltr Grey Water Waste Tank.
PP	x(1)	Water Pressure Pump.
SU	x(1)	2000mm Bench Top & Splashback, Single Drawer & Cupboards Under, Single Bowl & Drainer Sink (Cold Only).
BU	x(1)	Boiling Water Unit - Wall Mounted.
FR	x(1)	240 Ltr Fridge.
MW	x(1)	Microwave On Shelf.
TB	x(2)	Table With (6)x Chairs.
CT	x(1)	Formit MFT3 - Chemical Toilet With Built In Hand Basin.
fw	x(1)	Floor Waste.

Notes

- Built To Multitrade Building Hire Specifications.
- Heavy Duty Base Frame With Towing Points, 410UB51 Bearers, C10015 Floor Joists @ 600mm Ctrs.
- 19mm T&G F11 Plywood Flooring.
- 2mm Commercial R10 Vinyl Floor Covering, Coved 150mm Up Walls.
- 2400mm Internal Ceiling Height.
- Horizontal 'Panelrib' Profile External Colorbond Cladding.
- Zincalume 'Trimdek' Profile Roof Sheeting.
- Pre-finished Plywood Internal Wall & Ceiling Lining With PVC Joiners , Cornice, Skirting & Corner Moulds.
- Wall & Ceiling Insulation.
- Steel Mesh Flooring To External Services Area.
- Colorbond 'Panelrib' Soffit To External Service Area Ceiling.
- Steel Mesh Cage Around External Services Area.

Electrical Legend

Icon	Qty	Description
DSB	x(1)	Metal External Lockable Distribution Switchboard With Double Pole Main Switch, Double Pole Circuit Breakers Fitted With Cirlock Metal Lockouts.
PP	x(1)	Plug In Electrical Point Of Entry.
	x(3)	Light Switch (Double Pole).
	x(3)	10amp Single GPO (Double Pole).
2	x(2)	10amp Double GPO (Double Pole).
2WP	x(1)	Weatherproof 10amp Double GPO (Double Pole).
	x(2)	1200mm LED Internal Light Fitting.
	x(2)	600mm LED Internal Light Fitting.
	x(1)	600mm LED External Light Fitting.
	x(1)	1200mm LED External Light Fitting.
	x(1)	Wall Exhaust Fan.

CLIENT APPROVAL

Signature: Date:

Rev.	Description	Date	By
A	Issued For Client Review	14/02/20	BW

MULTITRADE BUILDING HIRE

THIS DRAWING AND DESIGN IS THE SOLE PROPERTY OF JABEGIL PTY LTD T/A MULTITRADE BUILDING HIRE A.B.N. 36 010 138 600 IT MAY NOT BE REPRODUCED, COPIED WHOLE OR IN PART WITHOUT WRITTEN AUTHORITY.

CLIENT		DATE
		14/02/20
TITLE: 7.2x3.0m SITE CRIB ROOM / TOILET - FLOOR PLAN		SCALE: 1:50
DESIGN WIND LOAD: C2 (W50C)	DRAWN: BW	CHECKED:
DRAWING NUMBER: SQF-3598-01	REVISION: A	SHEET SIZE: A3