PRELIMINARY DRAWING

## Colour Schedule

| External | | |
|---|---|---|
| Cladding | - | Surfmist |
| Roof | - | Zincalume |
| Capping | - | Surfmist |
| Doors | - | White |
| Windows | - | White |

| Internal | | |
|---|---|---|
| Vinyl | - | Grey |
| Walls | - | Grey |
| Ceiling | - | White |
| Cabinetry | - | White |

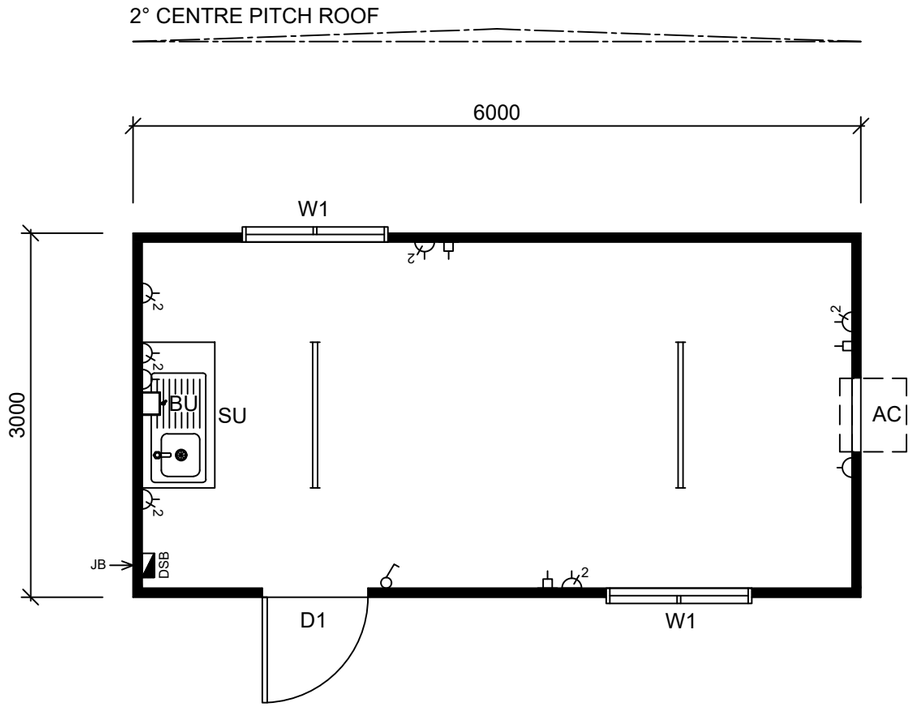


## 6.0x3.0m Crib Room - Floor Plan

Scale 1:50

## Item List

| Item | Qty | Description |
|---|---|---|
| D1 | x(1) | 2040x920mm External Metal Clad Door, Entrance Lockset. |
| W1 | x(2) | 900x1200mm Sliding Glass Window, Flyscreen. |
| AC | x(1) | 3.9kw TECO Wall Mounted Reverse Cycle Air Conditioner. |
| SU | x(1) | 1200mm Bench Top & Splashback, Cupboards Under, Single Bowl Single Drainer Sink (Cold Only). |
| BU | x(1) | 3L Boiling Water Unit - Wall Mounted. |

## Notes

- 75mm Steel Frame Construction.
- 150x75mm PFC Bearers.
- C10015 Floor Joists @ 600mm Ctrs.
- 19mm T&G F11 Plywood Flooring.
- 2mm Commercial Vinyl Floor Covering.
- 2400mm Internal Ceiling Height.
- Pre-finished Plywood Internal Wall & Ceiling Lining, PVC Joiners , Cornice, Skirting & Corner Moulds.
- Wall & Ceiling Insulation.
- Horizontal 'Panelrib' Profile External Colorbond Cladding.
- Zincalume 'Trimdek' Profile Roof Sheeting.
- Colorbond Barge Capping With Stop Ends.

## Electrical Legend

| Icon | Qty | Description |
|---|---|---|
| DSB | x(1) | Internal Lockable Distribution Switchboard, Double Pole Main Switch, Double Pole Breakers & Light Test Point. |
| JB | x(1) | Junction Box - Electrical Point Of Entry |
| | x(1) | Light Switch (Double Pole) |
| | x(2) | 10amp Single GPO (Double Pole) |
| 2 | x(6) | 10amp Double GPO (Double Pole) |
| | x(3) | Draw Wire With Blank Plate |
| | x(2) | 1200mm LED Batten Light Fitting. *(*Diffuser To Be Zip Tied)* |

CLIENT APPROVAL

Signature: Date:

| Rev. | Description | Date | By |
|---|---|---|---|
| A | Issued for Client Review | 18/06/24 | BW |
| | | | |
| | | | |
| | | | |
| | | | |

MULTITRADE BUILDING HIRE

THIS DRAWING AND DESIGN IS THE SOLE PROPERTY OF JABEGIL PTY LTD T/A MULTITRADE BUILDING HIRE A.B.N. 36 010 138 600 IT MAY NOT BE REPRODUCED, COPIED WHOLE OR IN PART WITHOUT WRITTEN AUTHORITY.

| CLIENT | | DATE |
|---|---|---|
| DENISON | | 18/06/24 |
| TITLE: 6.0x3.0m CRIB ROOM - FLOOR PLAN | | SCALE: 1:50 |
| DESIGN WIND LOAD: C2 (W50C) | DRAWN: BW | CHECKED: |
| DRAWING NUMBER: SQF-4370-02 | REVISION: A | SHEET SIZE: A3 |