PRELIMINARY DRAWING

## Colour Schedule

| External | | |
|---|---|---|
| Cladding | - | Surfmist |
| Roof | - | Zincalume |
| Capping | - | Surfmist |
| Gutters | - | Surfmist |
| Downpipes | - | Surfmist |
| Doors | - | White |
| Windows | - | White |

| Internal | | |
|---|---|---|
| Vinyl (R10) | - | Grey |
| Walls | - | Grey |
| Ceiling | - | White |

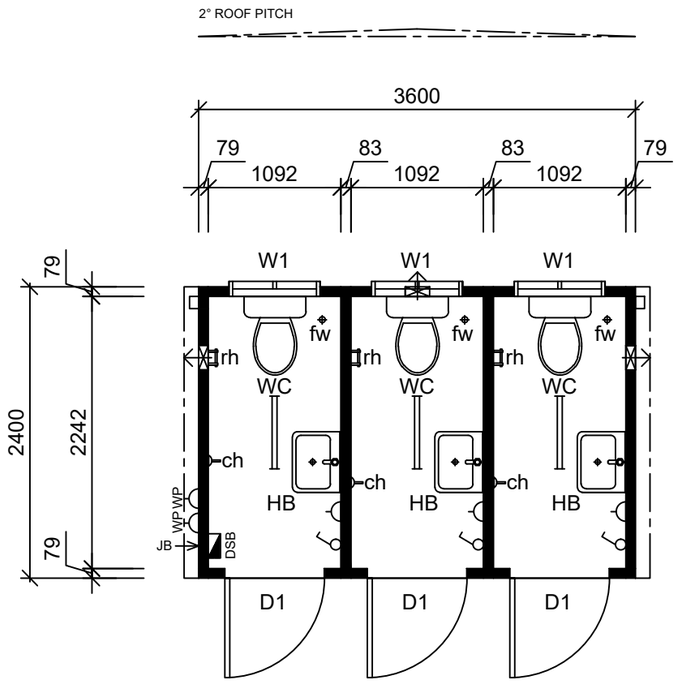


## 3.6x2.4m Toilet - Floor Plan

Scale 1:50

## Item List

| Item | Qty | Description |
|---|---|---|
| D1 | x(3) | 2040x820mm External Metal Clad Door, Privacy Set, Door Vent & Door Closer. |
| W1 | x(3) | 300x750mm Obscure Glass Sliding Window, Flyscreen. |
| WC | x(3) | Toilet Pan With Dual Flush Cistern. |
| HB | x(3) | Stainless Steel Hand Basin (Cold Only), Mirror Over. |
| rh | x(3) | Roll Holder. |
| ch | x(3) | Coat Hooks. |
| fw | x(3) | Floor Waste. |

## Notes

- 75mm Steel Frame Construction.
- 310UB32 Chassis Bearers.
- C10015 Floor Joists @ 600mm Ctrs.
- 19mm T&G F11 Plywood Flooring.
- 2mm Slip Resistant Vinyl Floor Covering, Coved In Wet Areas.
- 2400mm Internal Ceiling Height.
- Pre-finished Plywood Internal Wall & Ceiling Lining, PVC Joiners , Cornice & Corner Moulds.
- Wall & Ceiling Insulation.
- Colorbond 'Panelrib' Profile Horizontal Wall Cladding.
- Zincalume 'Trimdek' Profile Roof Sheeting.
- Colorbond Barge Capping, Gutters & Downpipes.
- Plumbing Waste To Be Harnessed To A Single Connection Point.

## Electrical Legend

| Icon | Qty | Description |
|---|---|---|
| DSB | x(1) | Internal Lockable Distribution Switchboard. |
| JB | x(1) | Junction Box - Point Of Entry. |
| | x(3) | Light Switch (Double Pole). |
| | x(3) | 10amp Single GPO (Double Pole). |
| WP | x(1) | External 10amp Single GPO (Double Pole). |
| | x(3) | 600mm LED Internal Light Fitting. |
| | x(3) | Wall Mounted Exhaust Fan. |

CLIENT APPROVAL

Signature: Date:

| Rev. | Description | Date | By |
|---|---|---|---|
| A | Issued for Client Review | 10/07/24 | AW |
| | | | |
| | | | |
| | | | |
| | | | |

MULTITRADE BUILDING HIRE

THIS DRAWING AND DESIGN IS THE SOLE PROPERTY OF TRANSPORTABLE BUILDINGS AUSTRALIA PTY LTD T/AS TRANSBUILD, ABN 45 082 023 354. IT MAY NOT BE REPRODUCED, COPIED WHOLE OR IN PART WITHOUT WRITTEN AUTHORITY.

| CLIENT | | DATE |
|---|---|---|
| GLADSTONE REGIONAL COUNCIL | | 10/07/24 |
| TITLE<br>3.6x2.4m TOILET<br>- FLOOR PLAN | | SCALE<br>1:50 |
| DESIGN WIND LOAD<br>C2 (W50C) | DRAWN<br>AW | CHECKED |
| DRAWING NUMBER<br>SQF-4384-01 | REVISION<br>A | SHEET SIZE<br>A3 |