PRELIMINARY DRAWING

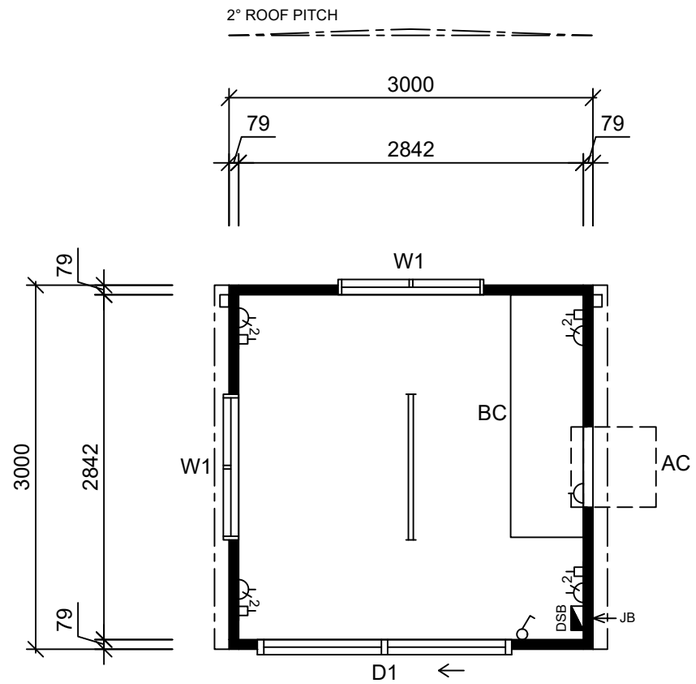

3.0x3.0m Office - Floor Plan

Scale 1:50

Colour Schedule

External		
Cladding	-	Surfmist
Roof	-	Zincalume
Capping	-	Surfmist
Gutters	-	Surfmist
Downpipes	-	Surfmist
Doors	-	Surfmist
Windows	-	Surfmist

Internal		
Vinyl	-	Grey
Walls	-	Grey
Ceiling	-	White
Cabinetry	-	White

Item List

Item	Qty	Description
D1	x(1)	2100x1800mm Sliding Glass Door, Flydoor.
W1	x(2)	900x1200mm Sliding Glass Window, Flyscreen.
AC	x(1)	3.9kw TECO Reverse Cycle Wall Mounted Air Conditioner.
BC	x(1)	2000mm Bench Top, Cupboards Under.

Notes

- 75mm Steel Frame Construction.
- 150x75mm PFC Chassis Bearers.
- 100x50x2mm RHS Floor Joists @ 600mm Ctrs.
- Hot Dipped Galv. Base Frame.
- 19mm T&G F11 Plywood Flooring.
- 2mm Commercial Vinyl Floor Covering.
- 2400mm Internal Ceiling Height.
- Pre-finished Plywood Internal Wall & Ceiling Lining, PVC Joiners, Cornice & Corner Moulds.
- Wall & Ceiling Insulation.
- Colorbond Ultra 'Panelrib' Profile Horizontal Wall Cladding.
- Zincalume 'Trimdek' Profile Roof Sheeting.
- Colorbond Ultra Barge Capping, Gutters & Downpipes.

Electrical Legend

Icon	Qty	Description
DSB	x(1)	Internal Lockable Distribution Switchboard, Double Pole Main Switch, Double Pole Breakers, Light Test Point.
JB	x(1)	Junction Box - Point Of Entry.
	x(1)	Light Switch (Double Pole).
	x(1)	10amp Single GPO (Double Pole).
2	x(4)	10amp Double GPO (Double Pole).
	x(4)	Draw Wire/Blank Plate.
	x(1)	1200mm LED Internal Light Fitting.

CLIENT APPROVAL

Signature: Date:

Rev.	Description	Date	By
A	Issued for Client Review	20/01/25	AW

MULTITRADE BUILDING HIRE

THIS DRAWING AND DESIGN IS THE SOLE PROPERTY OF TRANSPORTABLE BUILDINGS AUSTRALIA PTY LTD T/AS TRANSBUILD, ABN 45 082 023 354. IT MAY NOT BE REPRODUCED, COPIED WHOLE OR IN PART WITHOUT WRITTEN AUTHORITY.

CLIENT		DATE
KNL		20/01/25
TITLE: 3.0x3.0m OFFICE - FLOOR PLAN		SCALE: 1:50
DESIGN WIND LOAD: C3 - CYCLONIC	DRAWN: AW	CHECKED:
DRAWING NUMBER: SQF-4495-01	REVISION: A	SHEET SIZE: A3