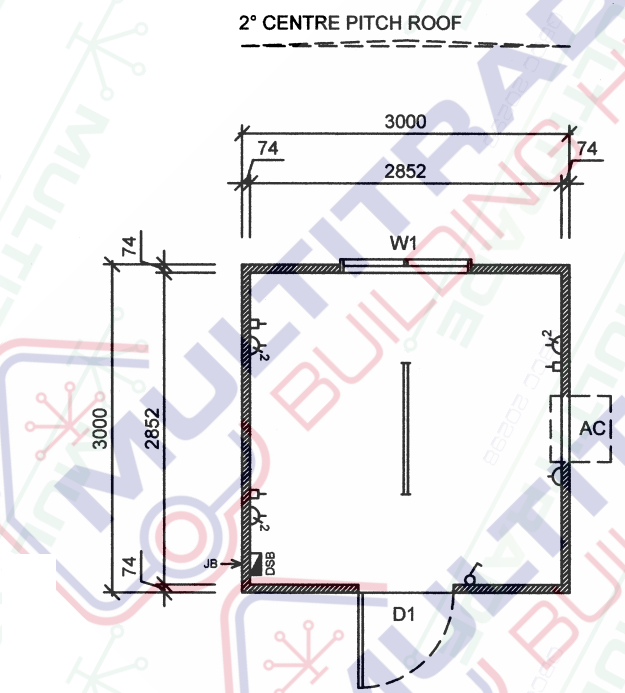


## 3.0x3.0m Office - Floor Plan

Scale 1:50

## Colour Schedule

**External**

| | | |
|---|---|---|
| Cladding | - | Surfmist |
| Roof | - | Zincalume |
| Flashings | - | Surfmist |
| Capping | - | Surfmist |
| Door | - | Surfmist |
| Window | - | White |

**Internal**

| | | |
|---|---|---|
| Vinyl | - | Grey |
| Walls | - | Grey |
| Ceiling | - | Mirage Pearl |

## Item List

| Item | Qty | Descripti | |
|---|---|---|---|
| D1 | x(1) | 2040x85( | External Metal Clad Door |
| W1 | x(1) | 900x120( | Sliding Glass Window - Grey Glass |
| AC | x(1) | Frame & | ut Only - For Wall Mounted Air Conditioner |
| | | (Cutout S | 605mm Wide x 385mm High) |

## Notes

- Built to Multitrade Building Hire Specification
- 2400mm Internal Ceiling Height

## Electrical Legend

| Icon | Qty | Description |
|---|---|---|
| DSB | x(1) | Distribution Switchboard |
| JB | x(1) | Junction Box - Electrical Point Of Entry |
| | x(1) | Light Switch |
| | x(1) | 10amp Single GPO |
| 2 | x(3) | 10amp Double GPO |
| | x(3) | Draw Wire With Blank Plate |
| | x(1) | 36 Watt Double Fluorescent Light |

CLIENT APPROVAL

Signature: Date:

| Rev. | Description | Date | By |
|---|---|---|---|
| A | Issued for Approval | 24/01/11 | B1 |

MULTITRADE BUILDING HIRE TRANSPORTABLES

MULTITRADE
6 SOUTH TREES DRIVE
PO BOX 8005
SOUTH GLADSTONE
4680, QLD, AUSTRALIA

Phone: 07 4979 2333
Fax: 07 4979 1698
Email: multitrade@hotkey.net.au

www.multitrade.com.au

THIS DRAWING AND DESIGN IS THE SOLE PROPERTY OF HALBIMBU PTY LTD T/A MULTITRADE A.B.N. 40 033 426 884 IT MAY NOT BE REPRODUCED, COPIED WHOLE OR IN PART WITHOUT WRITTEN AUTHORITY.

| CLIENT | | DATE |
|---|---|---|
| | | 24/01/11 |
| TITLE | | SCALE |
| 3.0x3.0m OFFICE | | 1:50 |
| DESIGN WIND LOAD | DRAWN | CHECKED |
| C2 - CYCLONIC | B1 | |
| DRAWING NUMBER | REVISION | SHEET SIZE |
| MBH-3030-OFF-01 | A | A3 |