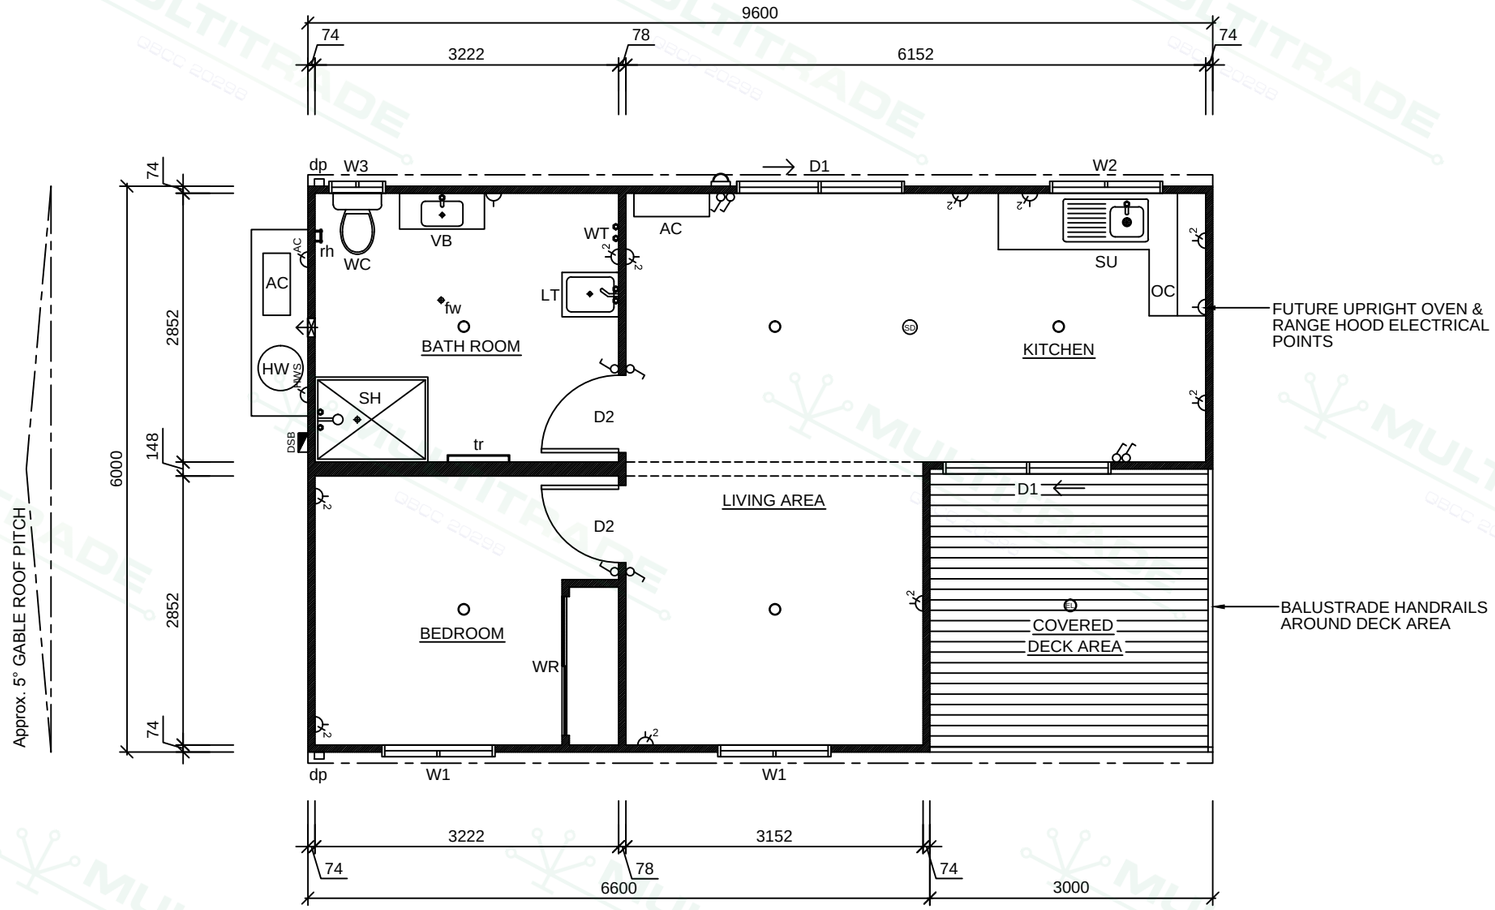

9.6x6.0m Single Bed Sitter Accommodation - Floor Plan

Scale 1:75

Colour Schedule

External

Cladding	-	Colorbond
Roof	-	Zincalume
Flashings	-	Colorbond
Capping	-	Colorbond
Gutter	-	Colorbond
Downpipe	-	Colorbond
Door	-	Colour
Windows	-	Colour

Internal

Vinyl	-	Colour
Vinyl (R10)	-	Colour
Walls	-	Grey or White
Ceiling	-	White
Doors	-	Grey or White
Cabinetry	-	Colour

Item List

Item	Qty	Description
D1	x(2)	2100x1800mm Sliding Glass Door - Grey Glass With Flydoor
D2	x(2)	2040x820mm Internal Painted Hollow Core Door
W1	x(2)	1200x1200mm Sliding Glass Window - Grey Glass, Flyscreen
W2	x(1)	900x1200mm Sliding Glass Window - Grey Glass, Flyscreen
W3	x(1)	900x600mm Obscure Glass Vented Window, Flyscreen
AC	x(1)	Reverse Cycle Split System Air Conditioner, Mounted On Chassis Extension.
SU	x(1)	2900mm Laminated Bench Top & Splashbacks, Cupboards & Set Of Drawers Under, Single Bowl Single Drainer Sink.
OC	x(1)	1300mm Overhead Cupboards With Microwave Provision.
OS	x(1)	Oven (Under Bench) With Hot Plates & Range Hood Over.
WR	x(1)	Built In Wardrobe With Sliding Doors, Top Shelf & Hanging Rail.
WC	x(1)	Toilet Pan With Dual Flush Cistern.
SH	x(1)	1200x900mm Shower With Glass Screen & Door.
VB	x(1)	900mm Wide Vanity Unit With Large Mirror Over.
HW	x(1)	Hot Water System - 160 Lt, Mounted On Chassis Extension .
LT	x(1)	Laundry Tub With Cabinet Under.
WT	x(1)	Washing Machine Taps (Provision For Washing Machine)
tr	x(1)	Double Towel Rail.
rh	x(1)	Roll Holder.
fw	x(1)	Floor Waste.
dp	x(2)	100x75mm Downpipe.

Electrical Legend

Icon	Qty	Description
DSB	x(1)	External Distribution Switchboard
	x(8)	Light Switch
	x(2)	10amp Single GPO
2	x(9)	10amp Double GPO
HWS	x(1)	External Isolator Switch - HWS
AC	x(1)	External Isolator Switch - AC
	x(5)	Internal Light Fitting
	x(1)	External Wall Light Fitting
	x(1)	External Ceiling Light Fitting
SD	x(1)	240 Volt Smoke Detector
	x(1)	Wall Mounted Exhaust Fan

Notes

- Built To Multitrade Building Hire Specifications
- 2400mm Internal Ceiling Height
- Coved R10 Slip Resistant Vinyl In Wet Areas
- Gutter & Downpipes

CLIENT APPROVAL

Signature: Date:

Rev.	Description	Date	By
A	Issued For Client Review	27/08/13	BW
B	Minor Changes	16/09/13	BW

MULTITRADE
BUILDING HIRE
TRANSPORTABLES

MULTITRADE
6 SOUTH TREES DRIVE
PO BOX 642
GLADSTONE
4680, QLD, AUSTRALIA

Phone: 07 4979 2333
Fax: 07 4979 1698
Email: multitrade@hotkey.net.au

www.multitrade.com.au

THIS DRAWING AND DESIGN IS THE SOLE PROPERTY OF JABEGIL PTY LTD T/A MULTITRADE BUILDING HIRE A.B.N. 36 010 138 600 IT MAY NOT BE REPRODUCED, COPIED WHOLE OR IN PART WITHOUT WRITTEN AUTHORITY.

		DATE: 16/09/13
TITLE: 9.6x6.0m SINGLE BED SITTER ACCOMMODATION		SCALE: 1:75
DESIGN WIND LOAD: C2 - CYCLONIC	DRAWN: BW	CHECKED:
DRAWING NUMBER: SQF-1571-01	REVISION: B	SHEET SIZE: A3