PRELIMINARY DRAWING

Colour Schedule

External		
Cladding	-	Surfmist
Roof	-	Zincalume
Capping	-	Surfmist
Gutter	-	Surfmist
Downpipe	-	Surfmist
Doors	-	White
Windows	-	White

Internal		
Vinyl	-	Grey
Walls	-	Grey
Ceiling	-	White

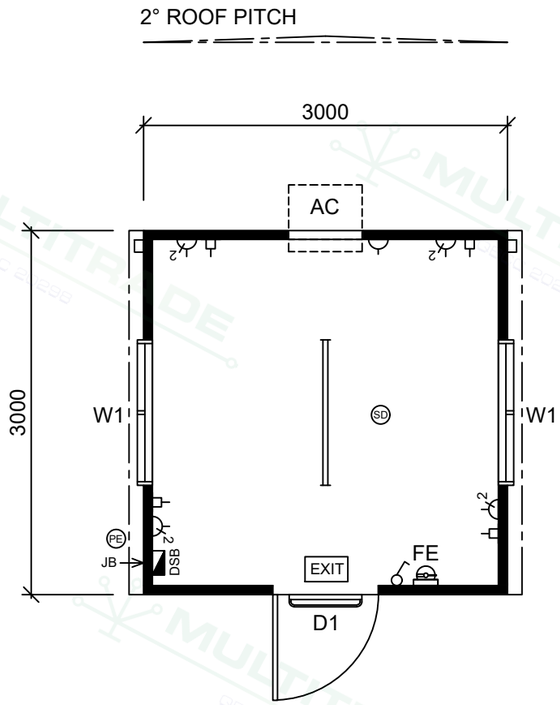

3.0x3.0m Open Plan Building - Floor Plan

Scale 1:50

Item List

Item	Qty	Description
D1	x(1)	2040x920mm External Metal Clad Door, Glass Viewing Panel, Door Closer, Entrance Lockset.
W1	x(2)	900x1200mm Sliding Glass Window, Flyscreen.
AC	x(1)	2.7kw TECO Wall Mounted Reverse Cycle Air Conditioner.
FE	x(1)	4.5kg DCP Fire Extinguisher & Sign.

Notes

- 75mm Steel Frame Construction.
- 150x75mm PFC Bearers
- C10015 Floor Joists @ 600mm Ctrs.
- 19mm T&G F11 Plywood Flooring.
- 2mm Commercial Vinyl Floor Covering.
- 2400mm Internal Ceiling Height.
- Pre-finished Plywood Internal Wall & Ceiling Lining, PVC Joiners, Cornice, Skirting & Corner Moulds.
- Wall & Ceiling Insulation.
- Horizontal 'Panelrib' Profile External Colorbond Cladding.
- Zincalume 'Trimdek' Profile Roof Sheeting.
- Colorbond Barge Capping, Gutter & Downpipe.

Electrical Legend

Icon	Qty	Description
DSB	x(1)	Metal Lockable Distribution Board, Double Pole 10kA Rated Main Switch, Double Pole 10kA Rated Breakers With Cirlock Breakers, Light Testing Point & Emergency Light Test Kit.
JB	x(1)	Junction Box - Electrical Point Of Entry.
	x(1)	Light Switch (Double Pole).
	x(1)	10amp Single GPO (Double Pole).
	x(4)	10amp Double GPO (Double Pole).
	x(4)	Draw Wire With Blank Plate.
	x(1)	1200mm LED Internal Light Fitting.
	x(1)	600mm LED External Light Fitting.
EXIT	x(1)	Emergency Exit Light.
SD	x(1)	Smoke Detector.
PE	x(1)	PE Cell.

CLIENT APPROVAL

Signature: Date:

Rev.	Description	Date	By
A	Issued for Client Review	22/08/23	BW

MULTITRADE BUILDING HIRE

THIS DRAWING AND DESIGN IS THE SOLE PROPERTY OF JABEGIL PTY LTD T/A MULTITRADE BUILDING HIRE A.B.N. 36 010 138 600 IT MAY NOT BE REPRODUCED, COPIED WHOLE OR IN PART WITHOUT WRITTEN AUTHORITY.

CLIENT		DATE
		22/08/23
TITLE: 3.0x3.0m OPEN PLAN BUILDING - FLOOR PLAN		SCALE: 1:50
DESIGN WIND LOAD: C2 (W50C)	DRAWN: BW	CHECKED:
DRAWING NUMBER: SQF-4235-01	REVISION: A	SHEET SIZE: A3