PRELIMINARY DRAWING

Colour Schedule

External		
Cladding	-	Surfmist
Roof	-	Zincalume
Capping	-	Surfmist
Gutters	-	Surfmist
Downpipes	-	Surfmist
Doors	-	Surfmist
Windows	-	Surfmist

Internal		
Vinyl (R10)	-	Grey
Walls	-	Grey
Ceiling	-	White
Partitions	-	White

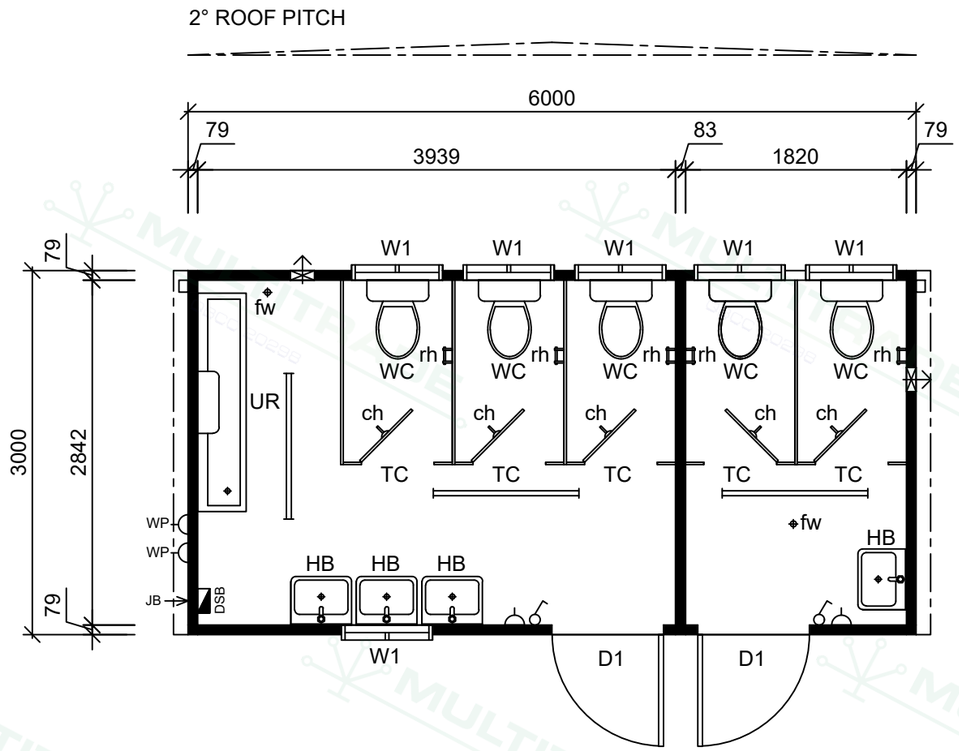

6.0x3.0m Male / Female Toilet - Floor Plan

Scale 1:50

Item List

Item	Qty	Description
D1	x(2)	2040x920mm External Metal Clad Door, Entrance Set, Door Closer & Gender Sign.
W1	x(6)	300x750mm Sliding Obscure Glass Window, Flyscreen.
WC	x(5)	Toilet Pan With Dual Flush Cistern.
TC	x(5)	Toilet Door & Partition.
HB	x(4)	Stainless Steel Hand Basin (Cold Only), Mirror Over.
UR	x(1)	1800mm Stainless Steel Wall Mounted Urinal & Cistern.
rh	x(5)	Roll Holder.
ch	x(5)	Coat Hooks.
fw	x(2)	Floor Waste.

Notes

- 75mm Steel Frame Construction.
- 310UB32 Chassis Bearers.
- C10015 Floor Joists @ 600mm Ctrs.
- 19mm T&G F11 Plywood Flooring.
- 2mm Slip Resistant Vinyl Floor Covering, Coved In Wet Areas.
- 2400mm Internal Ceiling Height.
- Pre-finished Plywood Internal Wall & Ceiling Lining, PVC Joiners , Cornice & Corner Moulds.
- Wall & Ceiling Insulation.
- Colorbond 'Panelrib' Profile Horizontal Wall Cladding.
- Zincalume 'Trimdek' Profile Roof Sheeting.
- Colorbond Barge Capping, Gutters & Downpipes.
- Plumbing Waste To Be Harnessed To A Single Connection Point.

Electrical Legend

Icon	Qty	Description
DSB	x(1)	Internal Lockable Distribution Switchboard, Double Pole Main Switch, Double Pole Breakers, Light Test Point.
JB	x(1)	Junction Box - Point Of Entry.
	x(2)	Light Switch (Double Pole).
	x(2)	10amp Single GPO (Double Pole).
WP	x(2)	External 10amp Single GPO (Double Pole).
	x(3)	1200mm LED Internal Light Fitting.
	x(2)	Wall Mounted Exhaust Fan.

CLIENT APPROVAL

Signature: Date:

Rev.	Description	Date	By
A	Issued for Client Review	04/07/24	AW

MULTITRADE BUILDING HIRE

THIS DRAWING AND DESIGN IS THE SOLE PROPERTY OF TRANSPORTABLE BUILDINGS AUSTRALIA PTY LTD T/AS TRANSBUILD, ABN 45 082 023 354. IT MAY NOT BE REPRODUCED, COPIED WHOLE OR IN PART WITHOUT WRITTEN AUTHORITY.

CLIENT	DATE
	04/07/24

TITLE	SCALE
6.0x3.0m MALE / FEMALE TOILET - FLOOR PLAN	1:50

DESIGN WIND LOAD	DRAWN	CHECKED
C2 (W50C)	AW	

DRAWING NUMBER	REVISION	SHEET SIZE
SQF-4381-02	A	A3