PRELIMINARY DRAWING

Colour Schedule

External		
Cladding	-	Surfmist
Roof	-	Zincalume
Capping	-	Surfmist
Gutters	-	Surfmist
Downpipes	-	Surfmist
Doors	-	White
Windows	-	White

Internal		
Vinyl	-	Grey
Walls	-	Grey
Ceiling	-	White
Doors	-	Grey

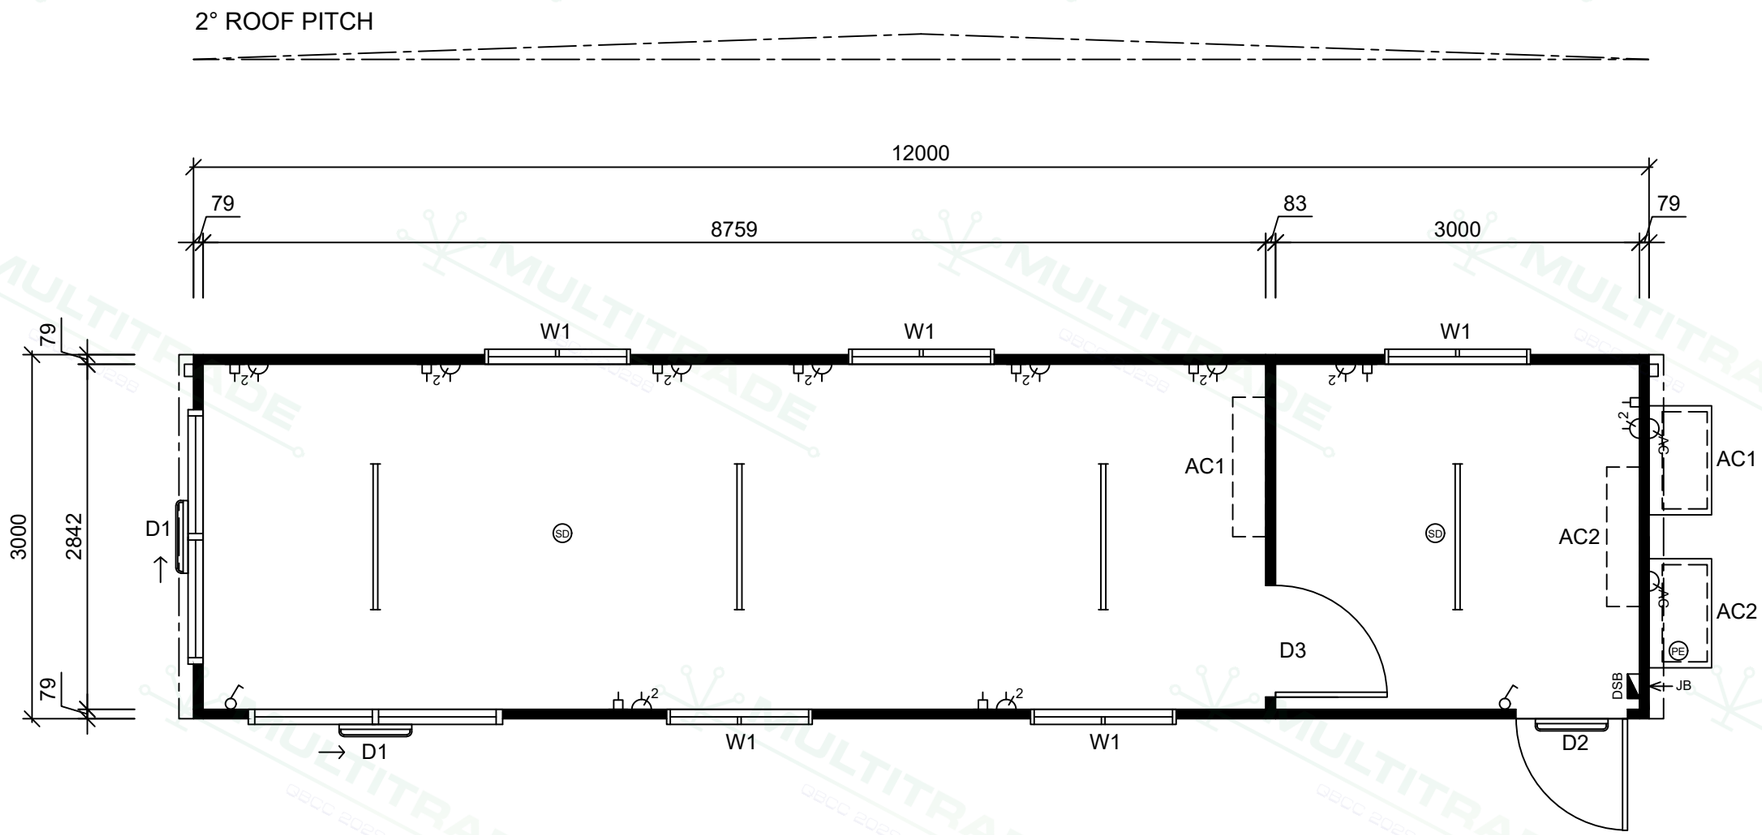

12.0x3.0m Office - Floor Plan

Scale 1:50

Item List

Item	Qty	Description
D1	x(2)	2100x2100mm Sliding Glass Door, Amplimesh Security Screen Door.
D2	x(1)	2040x920mm External Metal Clad Door, Glass Viewing Panel, Door Closer, Entrance Set.
D3	x(1)	2040x920mm Internal Painted Door, Entrance Set.
W1	x(5)	900x1200mm Sliding Glass Window, Amplimesh Security Window Screens.
AC1	x(1)	5.0kw MHI Reverse Cycle Split System Air Conditioner
AC2	x(1)	2.5kw MHI Reverse Cycle Split System Air Conditioner

**External Units Mounted On Chassis Extension.*

Notes

- 75mm Steel Frame Construction.
- 150x75mm PFC Chassis Bearers.
- C10015 Floor Joists @ 600mm Ctrs.
- 19mm T&G F11 Plywood Flooring.
- 2mm Commercial Vinyl Floor Covering.
- 2400mm Internal Ceiling Height.
- Pre-finished Plywood Internal Wall & Ceiling Lining, PVC Joiners , Cornice & Corner Moulds.
- Underfloor, Wall Batt, Ceiling Batt & Roof Blanket Insulation.
- Colorbond 'Panelrib' Profile Horizontal Wall Cladding.
- Zincalume 'Trimdek' Profile Roof Sheeting.
- Colorbond Barge Capping, Gutters & Downpipes.

Electrical Legend

Icon	Qty	Description
DSB	x(1)	Internal Lockable Distribution Switchboard, Double Pole Main Switch, Double Pole Breakers, Light Test Point.
JB	x(1)	Junction Box - Point Of Entry.
	x(2)	Light Switch (Double Pole).
2	x(10)	10amp Double GPO (Double Pole).
AC	x(2)	External Isolator Switch - Split AC.
	x(10)	Data Point
	x(4)	1200mm LED Internal Light Fitting.
	x(3)	600mm LED External Light Fitting.
SD	x(2)	Smoke Detector.
PE	x(1)	PE Cell.

CLIENT APPROVAL

Signature: Date:

Rev.	Description	Date	By
A	Issued for Client Review	11/11/24	AW

MULTITRADE BUILDING HIRE

THIS DRAWING AND DESIGN IS THE SOLE PROPERTY OF TRANSPORTABLE BUILDINGS AUSTRALIA PTY LTD T/AS TRANSBUILD, ABN 45 082 023 354. IT MAY NOT BE REPRODUCED, COPIED WHOLE OR IN PART WITHOUT WRITTEN AUTHORITY.

CLIENT	DATE
KINDERGARTEN	11/11/24
TITLE: 12.0x3.0m OFFICE - FLOOR PLAN	SCALE: 1:50

DESIGN WIND LOAD	DRAWN	CHECKED
C2 (W50C)	AW	

DRAWING NUMBER	REVISION	SHEET SIZE
SQF-4453-01	A	A3