


CONSTRUCTION DRAWING

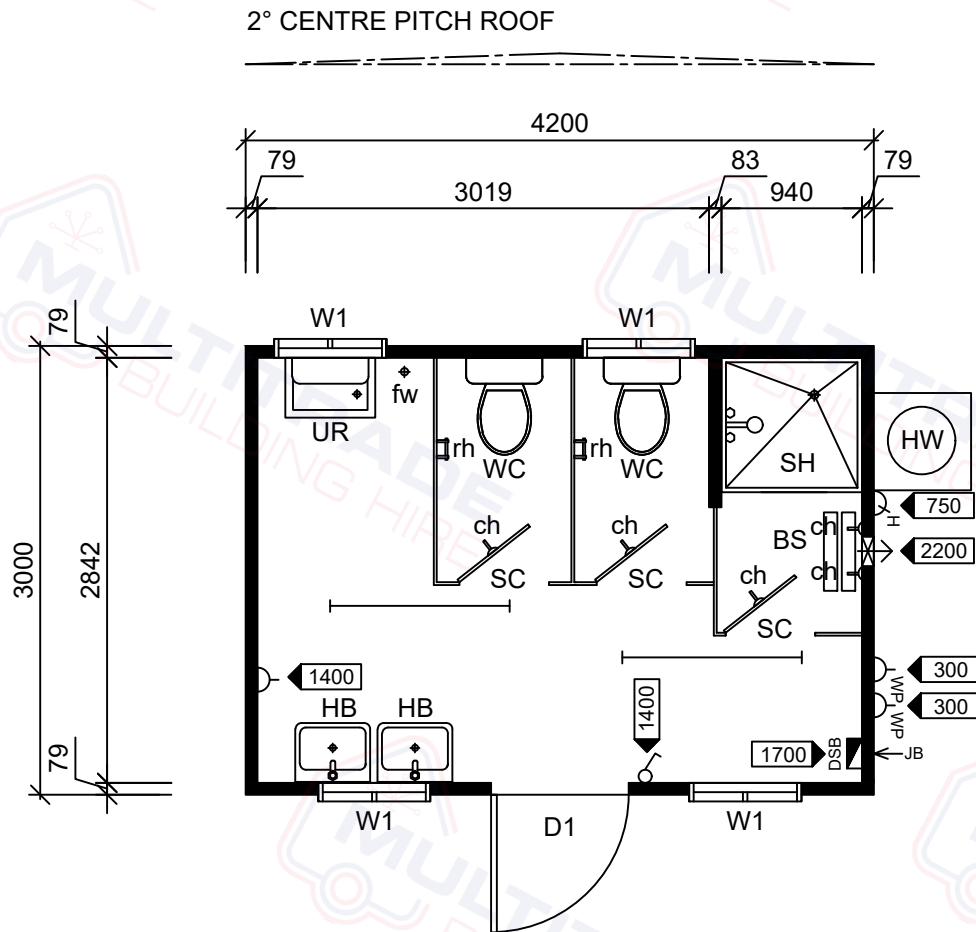

4.2x3.0m Ablution - Floor Plan

Scale 1:50

Colour Schedule

External		
Cladding	-	Surfmist
Roof	-	Zincalume
Capping	-	Surfmist
Doors	-	White
Windows	-	White

Internal		
Vinyl (R10)	-	Grey
Walls	-	Grey
Ceiling	-	White
Cabinetry	-	White

PROJECT NUMBER: PJF-654

SERIAL NUMBER: SN.1106

CLIENT APPROVAL

Signature: Date:

Rev.	Description	Date	By
0	Issued For Construction	30/06/21	BW



THIS DRAWING AND DESIGN IS THE SOLE PROPERTY OF TRANSPORTABLE BUILDINGS AUSTRALIA PTY LTD T/AS TRANSBUILD, ABN 45 082 023 354. IT MAY NOT BE REPRODUCED, COPIED WHOLE OR IN PART WITHOUT WRITTEN AUTHORITY.

CLIENT		DATE
		30/06/21
TITLE 4.2x3.0m ABLUTION - FLOOR PLAN		SCALE 1:50
DESIGN WIND LOAD C2 (W50C)	DRAWN BW	CHECKED
DRAWING NUMBER PJF-654-1106-01	REVISION 0	SHEET SIZE A3

Item List

Item	Qty	Description
D1	x(1)	2040x920mm External Metal Clad Door (Open Out), With Entrance Set & Door Closer.
W1	x(4)	300x750mm Obscure Glass Sliding Glass Window.
WC	x(2)	Toilet Pan With Dual Flush Cistern.
TC	x(2)	Toilet Door & Partition.
SH	x(1)	Fibreglass Shower With PVC Curtain.
SC	x(1)	Shower Door & Partition.
BS	x(1)	Bench Seat.
UR	x(1)	600mm Stainless Steel Wall Mountede Urinal With Cistern.
HB	x(2)	Stainless Steel Hand Basin (Hot & Cold) With Mirror Over.
HW	x(1)	80L Hot Water System, Mounted On Chassis Extension.
rh	x(1)	Roll Holder.
ch	x(5)	Coat Hook.
fw	x(1)	Floor Waste.

Notes

- 75mm Steel Frame Construction.
- 310UB32 Chassis Bearers / C10015 Floor Joists @ 600mm Ctrs.
- 19mm T&G F11 Plywood Flooring.
- 2mm Slip Resistant Vinyl Floor Covering, Coved In Wet Areas.
- 2400mm Internal Ceiling Height.
- Pre-finished Plywood Internal Wall & Ceiling Lining With PVC Joiners , Cornice & Corner Moulds.
- Wall & Ceiling Insulation.
- Horizontal 'Panelrib' Profile External Colorbond Cladding.
- Zincalume 'Trimdek' Profile Roof Sheeting.
- Colorbond Barge With Stop Ends.
- Plumbing Waste To Be Harnesssed To A Single Connection Point.

Electrical Legend

Icon	Qty	Description
DSB	x(1)	Internal Distribution Switchboard With Double Pole Main Switch, Double Pole Circuit Breakers & Light Test Point.
JB	x(1)	Junction Box - Electrical Point Of Entry.
LS	x(1)	Light Switch (Double Pole).
GPO	x(1)	10amp Single GPO (Double Pole).
WPGPO	x(2)	Weatherproof 10amp Single GPO (Double Pole).
ES	x(1)	External Isolator Switch - HWS.
LED	x(2)	1200mm LED Internal Light Fitting.
WF	x(1)	Wall Exhaust Fan.
Height		= Height Of Electrical Point