


PRELIMINARY DRAWING

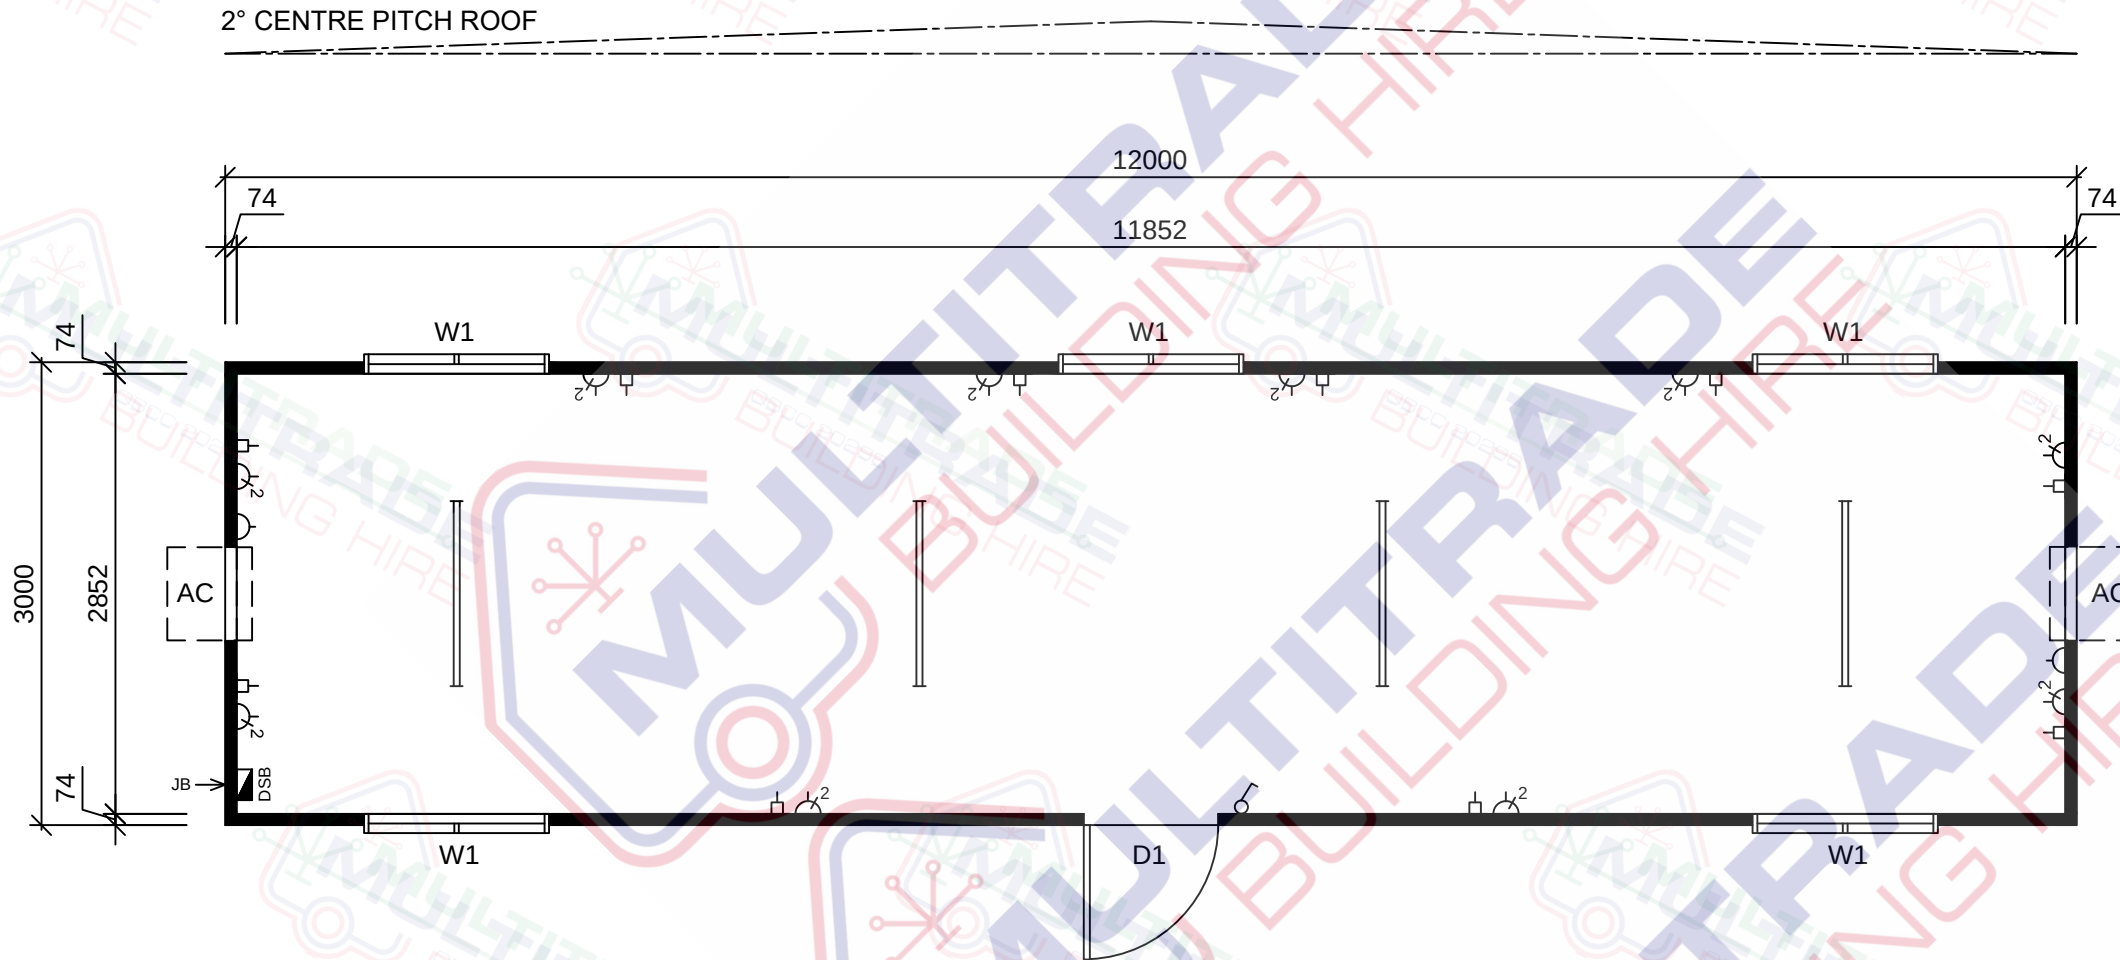

12.0x3.0m Office - Floor Plan

Scale 1:50

Item List

Item	Qty	Description
D1	x(1)	2040x920mm External Metal Clad Door.
W1	x(5)	900x1200mm Sliding Glass Window - Grey Glass With Flyscreen.
AC	x(2)	Provision For Wall Mounted Air Conditioner Unit.

Notes

- Built To Multitrade Building Hire Specifications.
- 150x75mm PFC Chassis Bearers With C10015 Floor Joists @ 600mm Ctrs.
- 19mm T&G F11 Plywood Flooring.
- 2mm Commercial Vinyl Floor Covering.
- 2400mm Internal Ceiling Height.
- Horizontal 'Panelrib' Profile External Colorbond Cladding.
- Zincalume 'Trimdek' Profile Roof Sheeting.
- Pre-finished Plywood Internal Wall & Ceiling Lining With PVC Joiners , Cornice, Skirting & Corner Moulds.
- Wall & Ceiling Insulation.

Electrical Legend

Icon	Qty	Description
	x(1)	Internal Distribution Switchboard
	x(1)	Junction Box - Electrical Point Of Entry
	x(1)	Light Switch
	x(2)	10amp Single GPO
	x(10)	10amp Double GPO
	x(10)	Draw Wire With Blank Plate
	x(4)	36 Watt Double Fluorescent Light

Colour Schedule

External		
Cladding	-	Surfmist
Roof	-	Zincalume
Capping	-	Surfmist
Gutter	-	Surfmist
Downpipe	-	Surfmist
Doors	-	White
Windows	-	White

Internal		
Vinyl	-	Grey
Walls	-	Grey
Ceiling	-	White
Cabinetry	-	White

CLIENT APPROVAL			
Signature:		Date:	
Rev.	Description	Date	By
A	Issued for Client Review	13/03/18	BW
THIS DRAWING AND DESIGN IS THE SOLE PROPERTY OF JABEGIL PTY LTD T/A MULTITRADE BUILDING HIRE A.B.N. 36 010 138 600 IT MAY NOT BE REPRODUCED, COPIED WHOLE OR IN PART WITHOUT WRITTEN AUTHORITY.			
		DATE	
		13/03/18	
TITLE		SCALE	
12.0x3.0m OFFICE		1:50	
DESIGN WIND LOAD	DRAWN	CHECKED	
C2 (W50C)	BW		
DRAWING NUMBER	REVISION	SHEET SIZE	
SQF-3208-01	A	A3	