


PRELIMINARY DRAWING

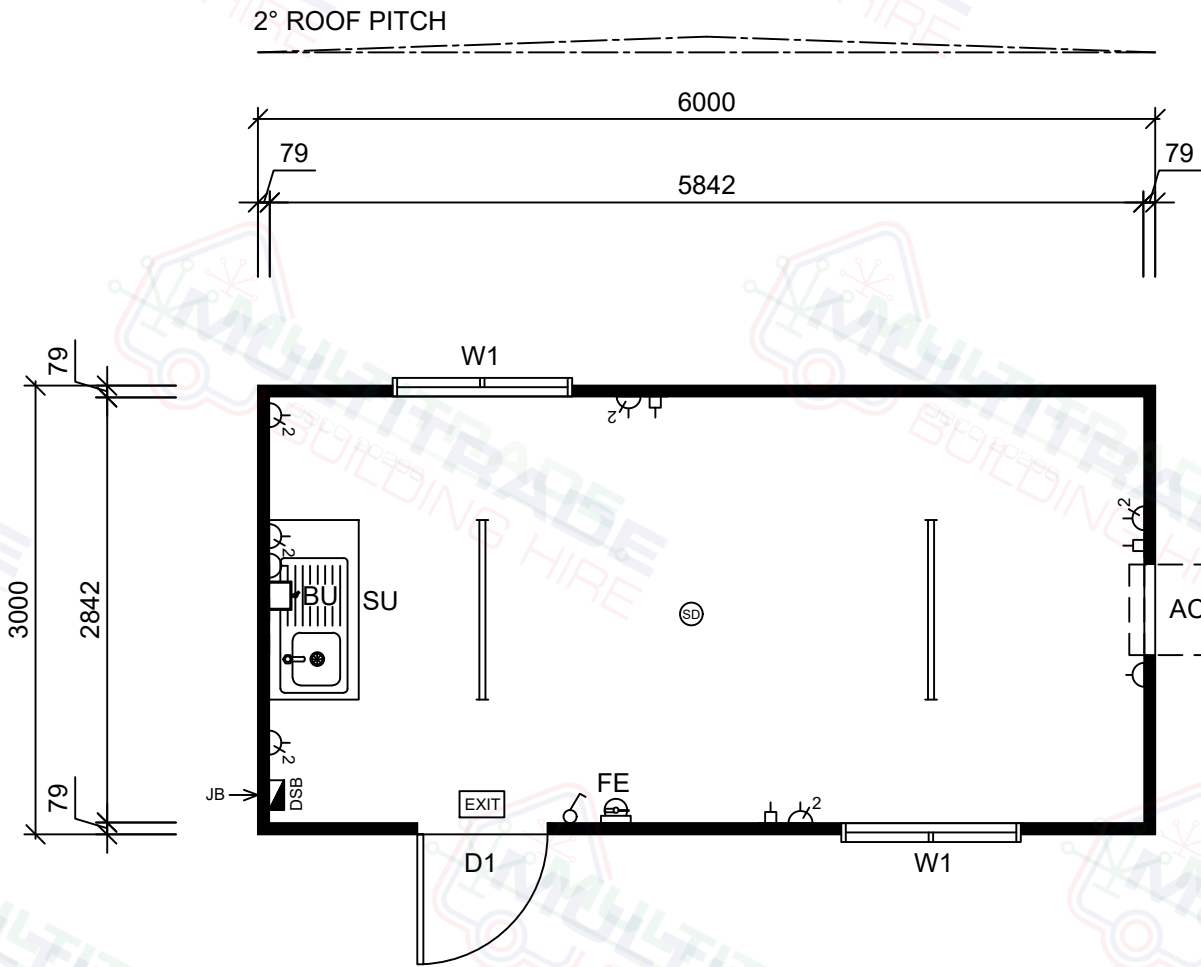

6.0x3.0m Crib Room - Floor Plan

Scale 1:50

Item List

Item	Qty	Description
D1	x(1)	2040x920mm External Metal Clad Door, Entrance Lockset.
W1	x(2)	900x1200mm Sliding Glass Window, Flyscreen.
AC	x(1)	3.9kw TECO Reverse Cycle Wall Mounted Air Conditioner.
SU	x(1)	1200mm Laminated Bench Top With Splshback, Cupboards Under, Single Bowl & Drainer Sink (Cold), 'P' Trap Waste.
BU	x(1)	3L Boiling Water Unit - Wall Mounted.
FE	x(1)	4.5kg Dry Chemical Fire Extinguisher & Sign.

Notes

- 75mm Steel Frame Construction.
- 150x75mm Bearers / C10015 Floor Joists @ 600mm Ctrs.
- 19mm T&G F11 Plywood Flooring.
- 2mm Commercial Vinyl Floor Covering.
- 2400mm Internal Ceiling Height.
- Pre-finished Plywood Internal Wall & Ceiling Linings, PVC Joiners, Skirting, Cornice & Corners Throughout.
- Wall & Ceiling Insulation.
- Horizontal 'Panelrib' Profile External Colorbond Cladding.
- Zincalume 'Trimdek' Profile Roof Sheeting.
- Colorbond Barge Capping With Stop Ends.

Electrical Legend

Icon	Qty	Description
	x(1)	Internal Metal Lockable Distribution Switchboard, 10kA Rated Double Pole Main Switch, 10kA Rated Double Pole Circuit Breakers With Cirlock Lockouts, Emergency Light Test Kit & Light Test Point.
	x(1)	Junction Box - Electrical Point Of Entry
	x(1)	Light Switch (Double Pole)
	x(2)	10amp Single GPO (Double Pole)
	x(6)	10amp Double GPO (Double Pole)
	x(4)	Draw Wire With Blank Plate
	x(2)	1200mm LED Batten Light Fitting.
	x(1)	Emergency Exit Light
	x(1)	Smoke Detector.

Colour Schedule

External		
Cladding	-	Surfmist
Roof	-	Zincalume
Capping	-	Surfmist
Door	-	White
Window	-	White
Internal		
Vinyl	-	Grey
Walls	-	Grey
Ceiling	-	White
Cabinetry	-	White

CLIENT APPROVAL

Signature: _____

Date: _____

Rev.	Description	Date	By
A	Approved For Construction	21/06/22	BW



THIS DRAWING AND DESIGN IS THE SOLE PROPERTY OF JABEGIL PTY LTD T/A MULTITRADE BUILDING HIRE A.B.N. 36 010 138 600 IT MAY NOT BE REPRODUCED, COPIED WHOLE OR IN PART WITHOUT WRITTEN AUTHORITY.

CLIENT		DATE
		21/06/22
TITLE		SCALE
6.0x3.0m CRIB ROOM - FLOOR PLAN		1:50
DESIGN WIND LOAD	DRAWN	CHECKED
C2 (W50C)	BW	
DRAWING NUMBER	REVISION	SHEET SIZE
SQF-4026-01	A	A3