


PRELIMINARY DRAWING

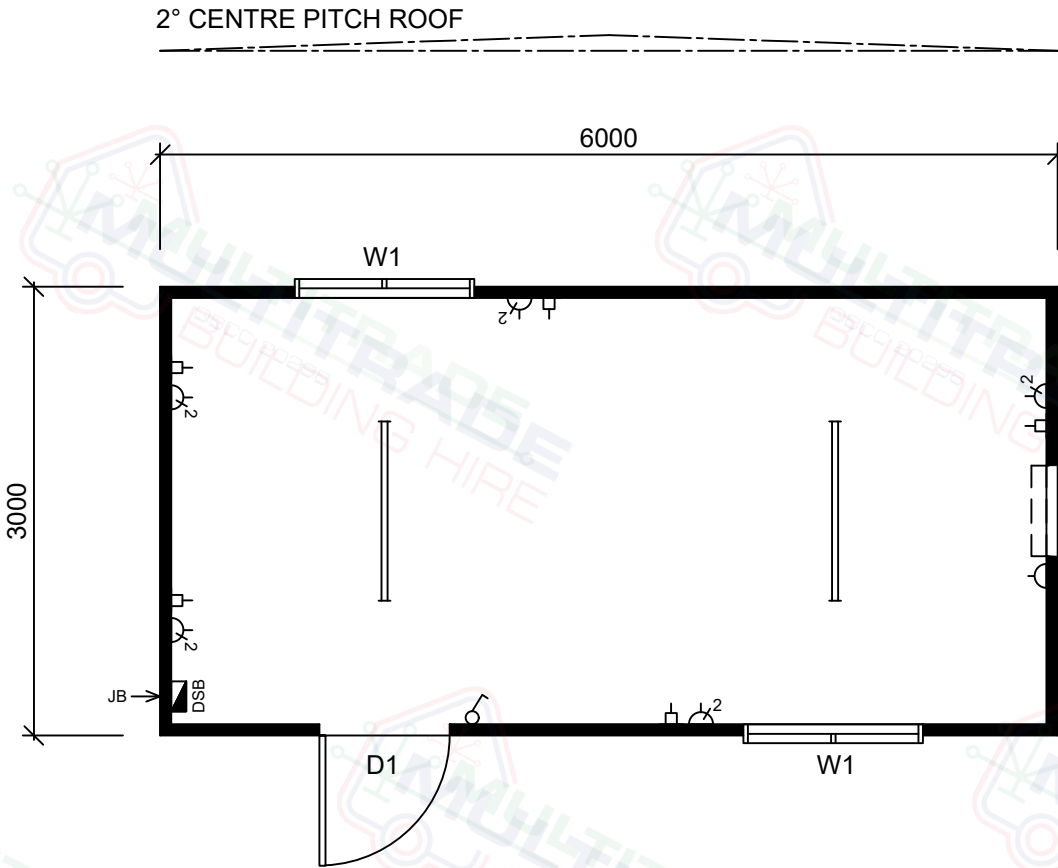

6.0x3.0m Office - Floor Plan

Scale 1:50

Item List

Item	Qty	Description
D1	x(1)	2040x920mm External Metal Clad Door, Entrance Lockset.
W1	x(2)	900x1200mm Sliding Glass Window, Flyscreen.
AC	x(1)	3.9kw TECO Wall Mounted Reverse Cycle Air Conditioner.

Notes

- 75mm Steel Frame Construction.
- 150x75mm PFC Bearers.
- C10015 Floor Joists @ 600mm Ctrs.
- 19mm T&G F11 Plywood Flooring.
- 2mm Commercial Vinyl Floor Covering.
- 2400mm Internal Ceiling Height.
- Pre-finished Plywood Internal Wall & Ceiling Lining, PVC Joiners , Cornice, Skirting & Corner Moulds.
- Wall & Ceiling Insulation.
- Horizontal 'Panelrib' Profile External Colorbond Cladding.
- Zincalume 'Trimdek' Profile Roof Sheetting.
- Colorbond Barge Capping With Stop Ends.

Electrical Legend

Icon	Qty	Description
	x(1)	Internal Lockable Distribution Switchboard, Double Pole Main Switch, Double Pole Breakers & Light Test Point.
	x(1)	Junction Box - Electrical Point Of Entry
	x(1)	Light Switch (Double Pole)
	x(1)	10amp Single GPO (Double Pole)
	x(5)	10amp Double GPO (Double Pole)
	x(5)	Draw Wire With Blank Plate
	x(2)	1200mm LED Batten Light Fitting. (*Diffuser To Be Zip Tied)

Colour Schedule

External	
Cladding	- Surfmist
Roof	- Zincalume
Capping	- Surfmist
Doors	- White
Windows	- White
Internal	
Vinyl	- Grey
Walls	- Grey
Ceiling	- White

CLIENT APPROVAL			
Signature:		Date:	
Rev.	Description	Date	By
A	Issued for Client Review	18/06/24	BW
THIS DRAWING AND DESIGN IS THE SOLE PROPERTY OF JABEGIL PTY LTD T/A MULTITRADE BUILDING HIRE A.B.N. 36 010 138 600 IT MAY NOT BE REPRODUCED, COPIED WHOLE OR IN PART WITHOUT WRITTEN AUTHORITY.			
CLIENT		DATE	
		18/06/24	
TITLE		SCALE	
6.0x3.0m OFFICE - FLOOR PLAN		1:50	
DESIGN WIND LOAD	DRAWN	CHECKED	
C2 (W50C)	BW		
DRAWING NUMBER	REVISION	SHEET SIZE	
SQF-4370-01	A	A3	