


PRELIMINARY DRAWING

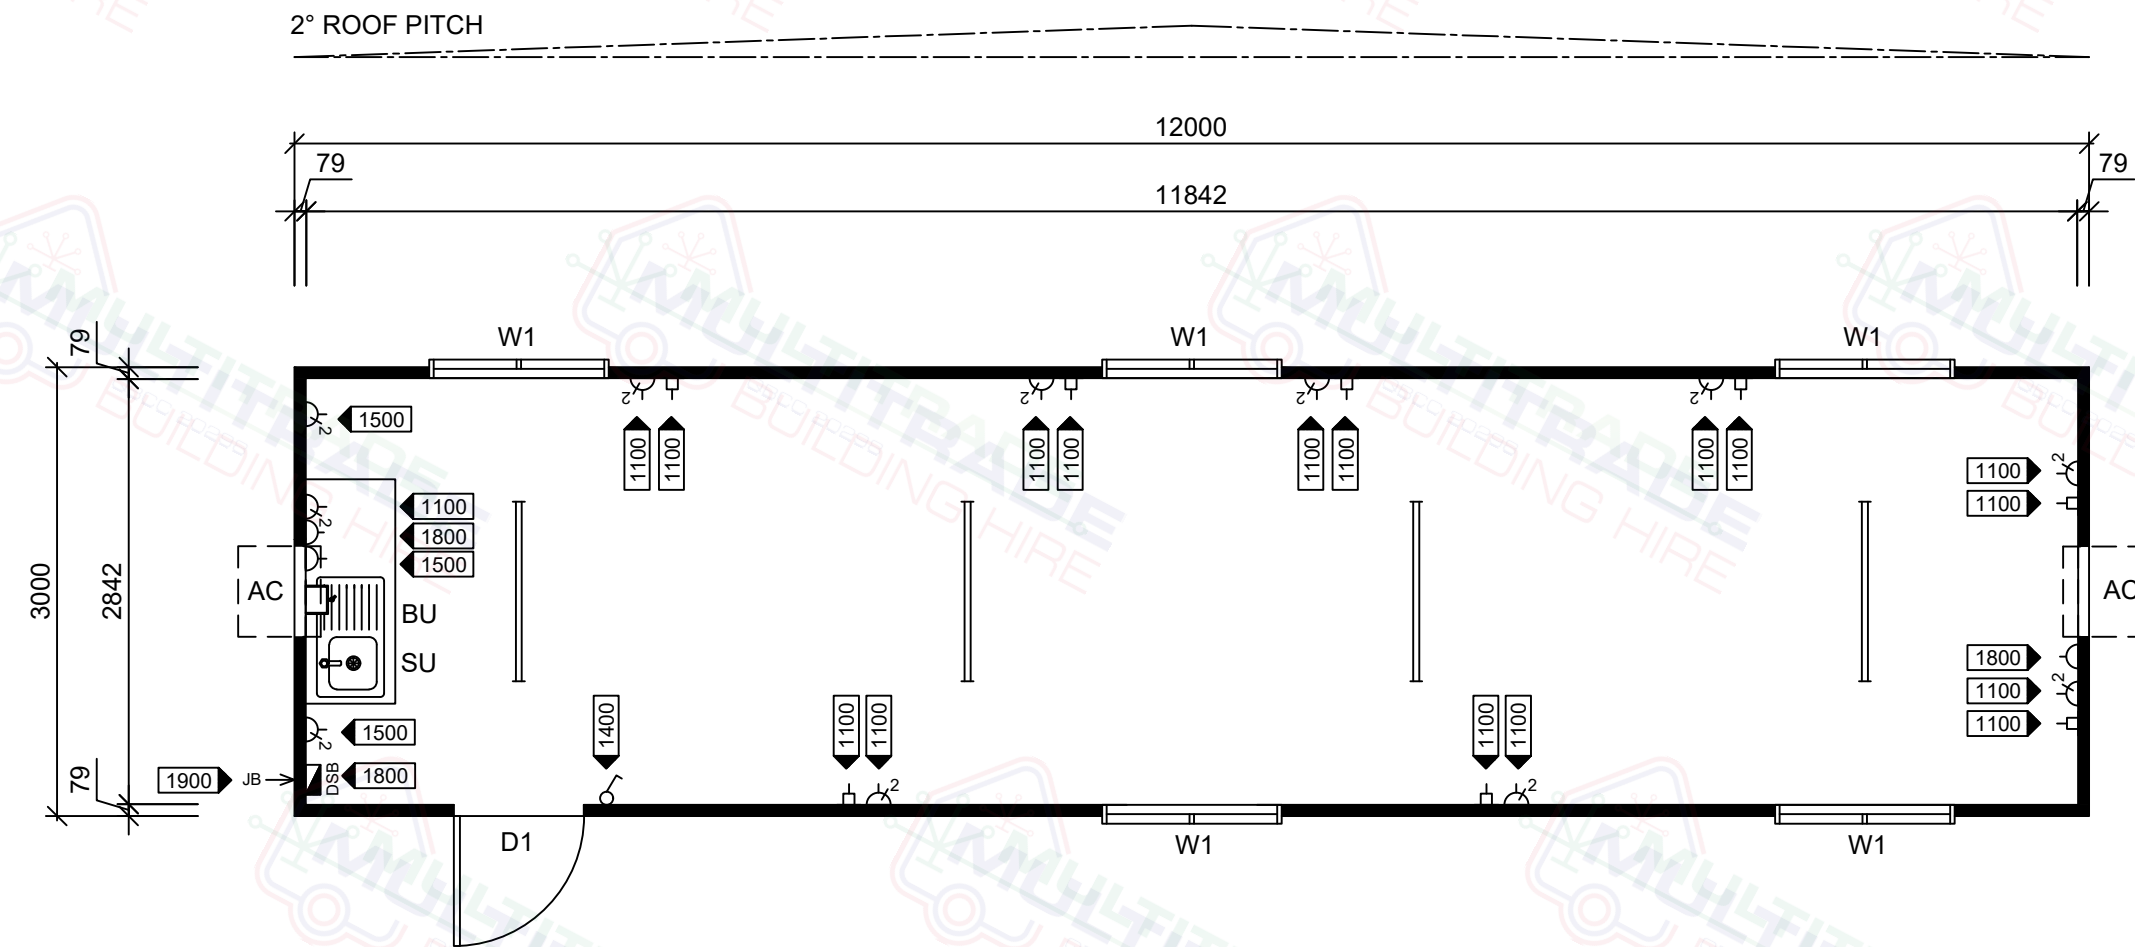

12.0x3.0m Crib Room - Floor Plan

Scale 1:50

Colour Schedule

External		
Cladding	-	Surfmist
Roof	-	Zincalume
Capping	-	Surfmist
Door	-	Surfmist
Window	-	Surfmist
Internal		
Vinyl	-	Grey
Walls	-	Grey
Ceiling	-	White
Cabinetry	-	White

CLIENT APPROVAL

Signature:		Date:	
Rev.	Description	Date	By
A	Issued for Client Review	18/07/24	BW



THIS DRAWING AND DESIGN IS THE SOLE PROPERTY OF JABEGIL PTY LTD T/A MULTITRADE BUILDING HIRE A.B.N. 36 010 138 600 IT MAY NOT BE REPRODUCED, COPIED WHOLE OR IN PART WITHOUT WRITTEN AUTHORITY.

CLIENT		DATE
		18/07/24
TITLE		SCALE
12.0x3.0m CRIB ROOM - FLOOR PLAN		1:50
DESIGN WIND LOAD	DRAWN	CHECKED
C2 (W50C)	BW	
DRAWING NUMBER	REVISION	SHEET SIZE
SQF-4392-01	A	A3

Item List

Item	Qty	Description
D1	x(1)	2040x920mm External Metal Clad Door, Entrance Lockset.
W1	x(5)	900x1200mm Sliding Glass Window, Flyscreen.
AC	x(2)	3.9kw TECO Reverse Cycle Mounted Air Conditioner.
SU	x(1)	1500mm Bench Top & Splashbacks, Cupboards & Single Drawer Under, Single Bowl Single Drainer Sink (Cold) - 'P' Trap Sink Waste Through Wall.
BU	x(1)	3L Boiling Water Unit - Wall Mounted.

Notes

- 75mm Steel Frame Construction.
- 150x75mm Chassis Bearers.
- C10015 Floor Joists @ 600mm Ctrs.
- 19mm T&G F11 Plywood Flooring.
- 2mm Commercial Vinyl Floor Covering.
- 2400mm Internal Ceiling Height.
- Pre-finished Plywood Internal Wall & Ceiling Linings, PVC Joiners, Skirting, Cornice & Corners Throughout.
- Wall & Ceiling Insulation.
- Colorbond 'Panelrib' Profile Horizontal Wall Cladding.
- Zincalume 'Trimdek' Profile Roof Sheeting.
- Colorbond Barge Capping With Stop Ends.

Electrical Legend

Icon	Qty	Description
DSB	x(1)	Lockable Internal Switchboard, Double Pole Main Switch, Double Pole Circuit Breakers, Light Test Point.
JB	x(1)	Junction Box - Electrical Point Of Entry
⏏	x(1)	Light Switch (Double Pole)
⏏ ²	x(3)	10amp Single GPO (Double Pole)
⏏ ²	x(11)	10amp Double GPO (Double Pole)
⏏	x(8)	Draw Wire & Blank Plate
⏏	x(4)	1200mm LED Batten Light Fitting
⏏	= Height Of Electrical Point	