


PRELIMINARY DRAWING

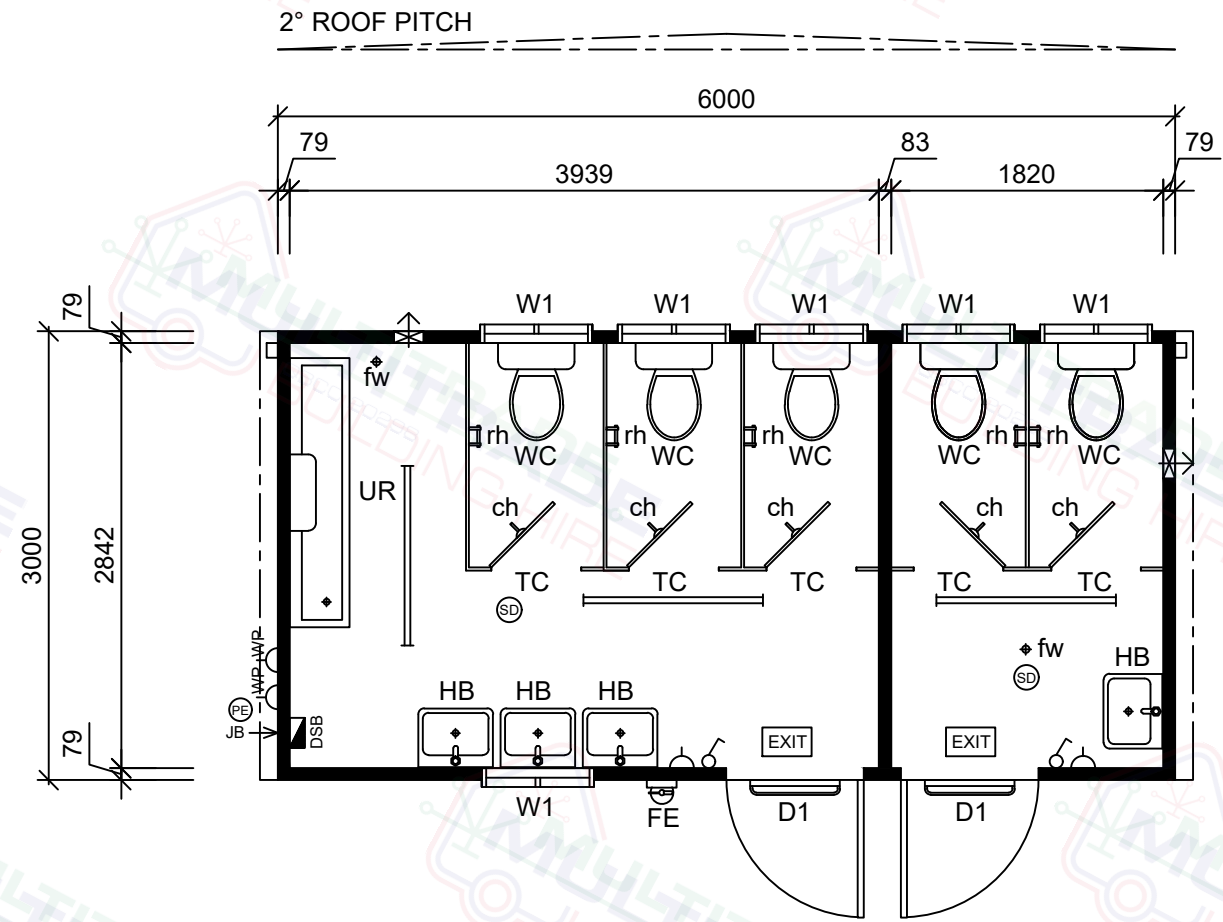

6.0x3.0m Male / Female Toilet - Floor Plan

Scale 1:50

Item List

Item	Qty	Description
D1	x(2)	2040x920mm External Metal Clad Door (Open Out), Entrance Set, Door Closer & Gender Sign.
W1	x(6)	300x750mm Obscure Glass Sliding Window, Flyscreen.
WC	x(5)	Toilet Pan, Dual Flush Cistern.
TC	x(5)	Toilet Door & Partition.
HB	x(4)	Stainless Steel Hand Basin (Cold Only), Mirror Over.
UR	x(1)	1800mm Stainless Steel Wall Mounted Urinal & Cistern.
rh	x(5)	Roll Holder.
ch	x(5)	Coat Hooks.
fw	x(2)	Floor Waste.
FE	x(1)	4.5kg DCP Fire Extinguisher & Sign.

Notes

- 75mm Steel Frame Construction.
- 310UB32 Chassis Bearers.
- C10015 Floor Joists @ 600mm Ctrs.
- 19mm T&G F11 Plywood Flooring.
- 2mm Slip Resistant Vinyl Floor Covering, Coved In Wet Areas.
- 2400mm Internal Ceiling Height.
- Pre-finished Plywood Internal Wall & Ceiling Lining, PVC Joiners, Cornice & Corner Moulds.
- Wall & Ceiling Insulation.
- Colorbond 'Panelrib' Profile Horizontal Wall Cladding.
- Zincolume 'Trimdek' Profile Roof Sheeting.
- Colorbond Barge Capping, Gutters & Downpipes
- Plumbing Waste To Be Harnessed To A Single Connection Point.

Electrical Legend

Icon	Qty	Description
	x(1)	Metal Lockable Distribution Board, Double Pole 10kA Rated Main Switch, Double Pole 10kA Rated Breakers With Cirlock Breakers, Light Testing Point & Emergency Light Test Kit.
	x(1)	Junction Box - Electrical Point Of Entry
	x(2)	Light Switch (Double Pole).
	x(2)	10amp Single GPO (Double Pole).
	x(2)	External 10amp Single GPO (Double Pole).
	x(3)	1200mm LED Batten Light Fitting.
	x(2)	600mm LED External Light Fitting.
	x(2)	Emergency Exit Light.
	x(1)	Smoke Detector.
	x(1)	PE Cell.
	x(2)	Wall Exhaust Fan.

Colour Schedule

External	
Cladding	- Surfmist
Roof	- Zincolume
Capping	- Surfmist
Gutter	- Surfmist
Downpipe	- Surfmist
Doors	- White
Windows	- White

Internal	
Vinyl (R10)	- Grey
Walls	- Grey
Ceiling	- White
Cabinetry	- White

CLIENT APPROVAL

Signature:

Date:

Rev.	Description	Date	By
A	Issued for Client Review	28/11/24	BW



THIS DRAWING AND DESIGN IS THE SOLE PROPERTY OF JABEGIL PTY LTD T/A MULTITRADE BUILDING HIRE A.B.N. 36 010 138 600 IT MAY NOT BE REPRODUCED, COPIED WHOLE OR IN PART WITHOUT WRITTEN AUTHORITY.

		DATE
		28/11/24
TITLE		SCALE
6.0x3.0m MALE / FEMALE TOILET - FLOOR PLAN		1:50
DESIGN WIND LOAD	DRAWN	CHECKED
C2 (W50C)	BW	
DRAWING NUMBER	REVISION	SHEET SIZE
SQF-4477-01	A	A3