


PRELIMINARY DRAWING

Colour Schedule

External		
Cladding	-	Surfmist
Roof	-	Zincalume
Capping	-	Surfmist
Gutters	-	Surfmist
Downpipes	-	Surfmist
Doors	-	Surfmist
Windows	-	Surfmist

Internal		
Vinyl	-	Grey
Walls	-	Grey
Ceiling	-	White
Cabinetry	-	White

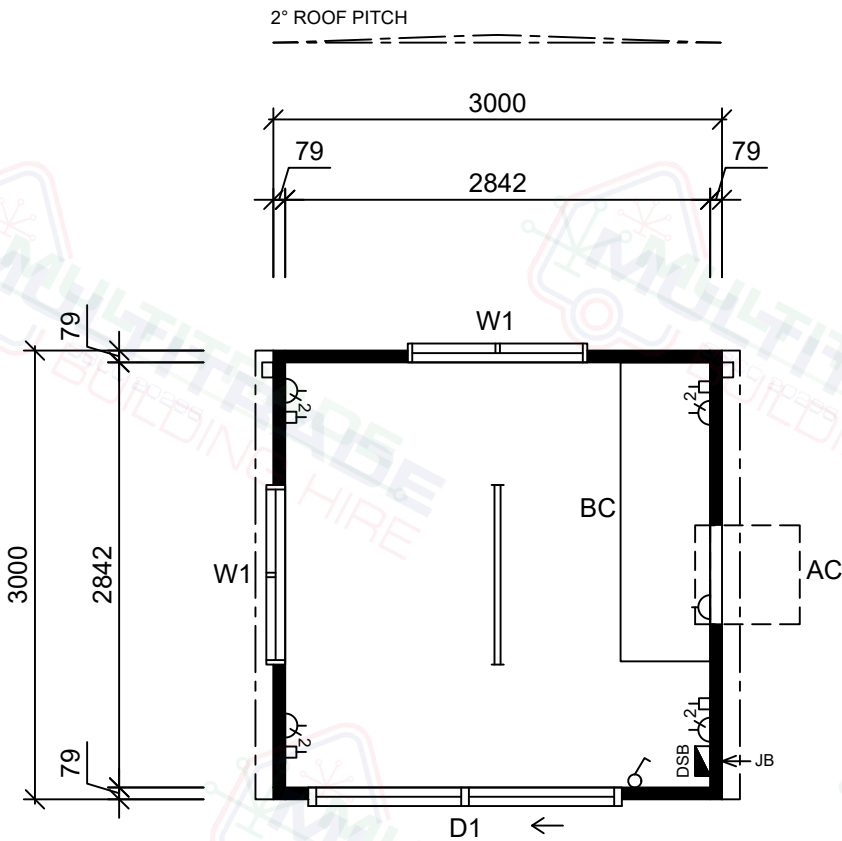

3.0x3.0m Office - Floor Plan

Scale 1:50

Item List

Item	Qty	Description
D1	x(1)	2100x1800mm Sliding Glass Door, Flydoor.
W1	x(2)	900x1200mm Sliding Glass Window, Flyscreen.
AC	x(1)	3.9kw TECO Reverse Cycle Wall Mounted Air Conditioner.
BC	x(1)	2000mm Bench Top, Cupboards Under.

Notes

- 75mm Steel Frame Construction.
- 150x75mm PFC Chassis Bearers.
- 100x50x2mm RHS Floor Joists @ 600mm Ctrs.
- Hot Dipped Galv. Base Frame.
- 19mm T&G F11 Plywood Flooring.
- 2mm Commercial Vinyl Floor Covering.
- 2400mm Internal Ceiling Height.
- Pre-finished Plywood Internal Wall & Ceiling Lining, PVC Joiners, Cornice & Corner Moulds.
- Wall & Ceiling Insulation.
- Colorbond Ultra 'Panelrib' Profile Horizontal Wall Cladding.
- Zincalume 'Trimdek' Profile Roof Sheeting.
- Colorbond Ultra Barge Capping, Gutters & Downpipes.

Electrical Legend

Icon	Qty	Description
DSB	x(1)	Internal Lockable Distribution Switchboard, Double Pole Main Switch, Double Pole Breakers, Light Test Point.
JB	x(1)	Junction Box - Point Of Entry.
Light Switch	x(1)	Light Switch (Double Pole).
10amp Single GPO	x(1)	10amp Single GPO (Double Pole).
10amp Double GPO	x(4)	10amp Double GPO (Double Pole).
Draw Wire/Blank Plate	x(4)	Draw Wire/Blank Plate.
1200mm LED Internal Light Fitting	x(1)	1200mm LED Internal Light Fitting.

CLIENT APPROVAL

Signature: _____ Date: _____

Rev.	Description	Date	By
A	Issued for Client Review	20/01/25	AW



THIS DRAWING AND DESIGN IS THE SOLE PROPERTY OF TRANSPORTABLE BUILDINGS AUSTRALIA PTY LTD T/AS TRANSBUILD, ABN 45 082 023 354. IT MAY NOT BE REPRODUCED, COPIED WHOLE OR IN PART WITHOUT WRITTEN AUTHORITY.

CLIENT	DATE
	20/01/25
TITLE	SCALE
3.0x3.0m OFFICE - FLOOR PLAN	1:50
DESIGN WIND LOAD	DRAWN
C3 - CYCLONIC	AW
CHECKED	
DRAWING NUMBER	REVISION
SQF-4495-01	A
SHEET SIZE	A3