


CONSTRUCTION DRAWING

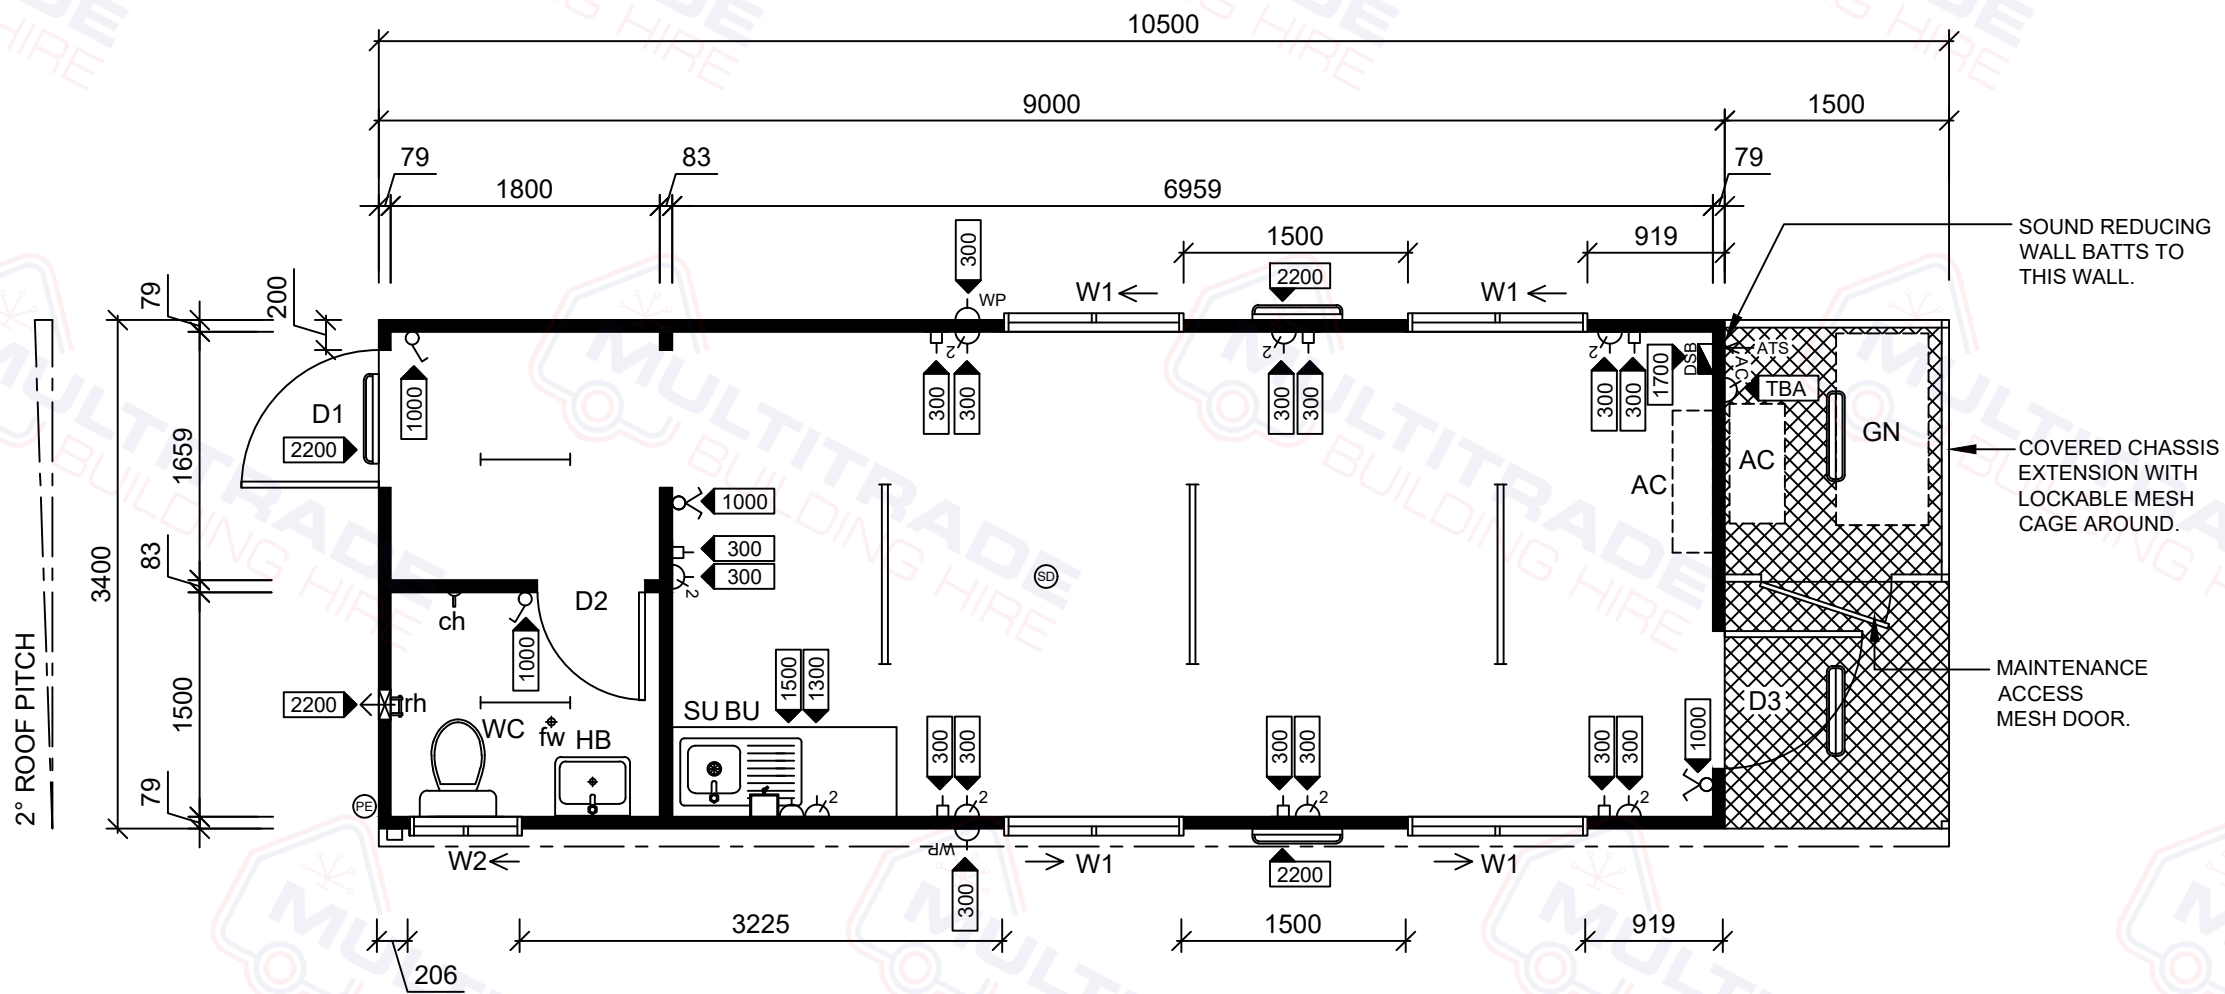

10.5x3.4m Gatehouse - Floor Plan

Scale 1:50

Item List

Item	Qty	Description
D1	x(1)	2040x920mm External Metal Clad Door, Door Closer, Entrance Lockset.
D2	x(1)	2040x720mm Internal Painted Hollow Core Door, Privacy Set, Door Closer & Toilet Sign.
D3	x(1)	2095x910mm Commercial Glass Aluminium Framed Door, Door Closer, Entrance Lockset.
W1	x(4)	900x1200mm Sliding Glass Window (*No Flyscreen).
W2	x(1)	300x750mm Sliding Obscure Glass Window (*No Flyscreen).
AC	x(1)	5.0kw MHI Inverter Reverse Cycle Split System Air Conditioner. *Note: External AC Units Mounted On Chassis Extension.
SU	x(1)	1500mm Bench Top & Splashback, Single Drawer & Cupboards Under, Single Bowl Single Drainer Sink (Cold).
BU	x(1)	3L ZIP Boiling Water Unit - Wall Mounted.
WC	x(1)	Toilet Pan With Dual Flush Cistern.
HB	x(1)	Wall Mounted Hand Basin (Cold), Mirror Over.
rh	x(1)	Roll Holder.
ch	x(1)	Coat Hook.
fw	x(1)	Floor Waste.
GN	x(1)	Kubota GL9000-AU-B, 9kVa Single Phase Diesel Generator, 28L Fuel Tank (*Approx. 8 Hours Run Time).

Notes

- 75mm Steel Frame Construction.
- 150x75mm PFC Bearers.
- C10015 Floor Joists @ 600mm Ctrs.
- 19mm T&G F11 Plywood Flooring.
- 2mm Commercial Vinyl Floor Covering.
- 2mm Slip Resistant Vinyl Floor Covering, Coved In Wet Areas.
- 2400mm Internal Ceiling Height.
- Pre-finished Plywood Internal Wall & Ceiling Lining With PVC Joiners , Cornice, Skirting & Corner Moulds.
- Underfloor, Wall Batt, Ceiling Batt & Roof Blanket Insulation.
- Colorbond 'Panelrib' Profile Horizontal Wall Cladding.
- Colorbond 'Trimdek' Profile Roof Sheeting.
- Colorbond Barge Capping, Gutters & Downpipes.

Electrical Legend

Icon	Qty	Description
	x(1)	Internal Lockable Distribution Switchboard Double Pole Main Switch, Double Pole Circuit Breakers & Light Test Point.
	x(1)	ATS / Electrical Point Of Entry
	x(2)	Two Way Light Switch (Double Pole)
	x(1)	Light Switch (Double Pole)
	x(1)	10amp Single GPO (Double Pole)
	x(8)	10amp Double GPO (Double Pole)
	x(2)	Weatherproof 10amp Single GPO (Double Pole)
	x(1)	External Isolator Switch - AC (Double Pole)
	x(6)	Draw Wire With Blank Plate
	x(3)	1200mm LED External Light Fitting.
	x(2)	600mm LED Internal Light Fitting.
	x(5)	600mm LED External Light Fitting.
	x(1)	Wall Mounted Exhaust Fan.
	x(1)	Smoke Detector.
	x(1)	PE Cell.
		= Height Of Electrical Point

Colour Schedule

External		
Cladding	-	Deep Ocean
Roof	-	Surfmist
Capping	-	Deep Ocean
Gutter	-	Deep Ocean
Downpipe	-	Deep Ocean
Doors	-	Deep Ocean
Windows	-	Black

Internal		
Vinyl	-	Grey
Vinyl (R10)	-	Grey
Walls	-	Grey
Ceiling	-	White
Cabinetry	-	White
Door	-	Grey

PROJECT NUMBER: PJF-764

SERIAL NUMBER: SN.1416

CLIENT APPROVAL

Signature: _____ Date: _____

Rev.	Description	Date	By
0	Issued For Construction	20/03/23	BW
1	Update Drawing Details	15/05/23	BW
2	Changes Requested	25/05/23	BW



THIS DRAWING AND DESIGN IS THE SOLE PROPERTY OF TRANSPORTABLE BUILDINGS AUSTRALIA PTY LTD T/AS TRANSBUILD, ABN 45 082 023 354. IT MAY NOT BE REPRODUCED, COPIED WHOLE OR IN PART WITHOUT WRITTEN AUTHORITY.

CLIENT		DATE
(HALL CONTRACTING)		25/05/23
TITLE		SCALE
10.5x3.4m GATEHOUSE - FLOOR PLAN		1:50
DESIGN WIND LOAD	DRAWN	CHECKED
N3 (W41N)	BW	
DRAWING NUMBER	REVISION	SHEET SIZE
PJF-764-1416-01	2	A3