


PRELIMINARY DRAWING

Colour Schedule

External	
Cladding	- Surfmist
Roof	- Zinalume
Capping	- Surfmist
Gutters	- Surfmist
Downpipes	- Surfmist
Doors	- White
Windows	- White

Internal	
Vinyl (R10)	- Grey
Walls	- Grey
Ceiling	- White

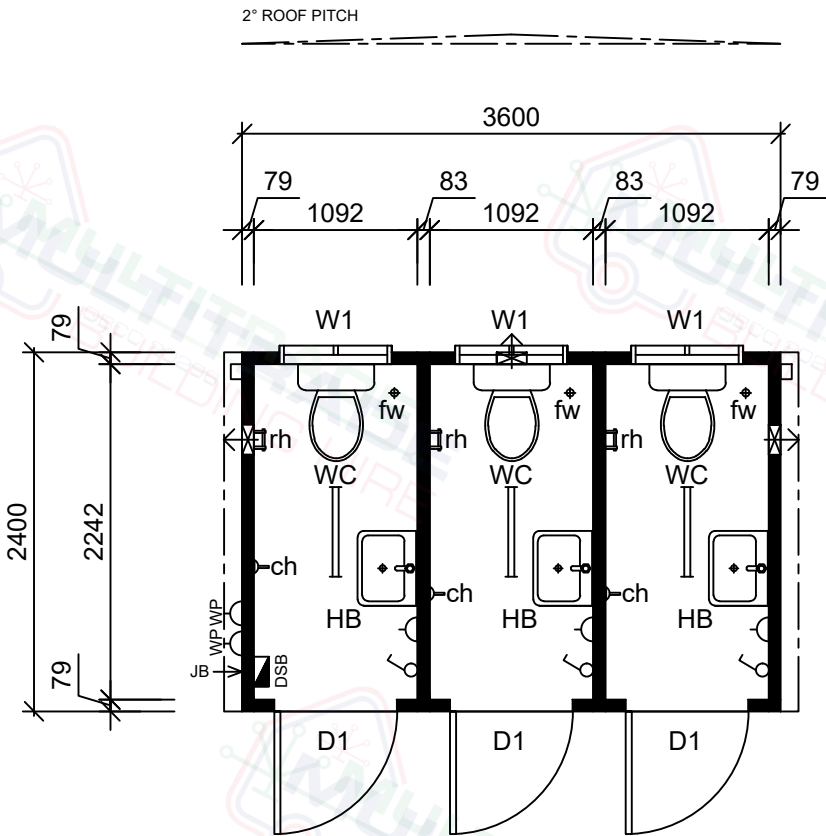

3.6x2.4m Toilet - Floor Plan

Scale 1:50

Item List

Item	Qty	Description
D1	x(3)	2040x820mm External Metal Clad Door, Privacy Set, Door Vent & Door Closer.
W1	x(3)	300x750mm Obscure Glass Sliding Window, Flyscreen.
WC	x(3)	Toilet Pan With Dual Flush Cistern.
HB	x(3)	Stainless Steel Hand Basin (Cold Only), Mirror Over.
rh	x(3)	Roll Holder.
ch	x(3)	Coat Hooks.
fw	x(3)	Floor Waste.

Notes

- 75mm Steel Frame Construction.
- 310UB32 Chassis Bearers.
- C10015 Floor Joists @ 600mm Ctrs.
- 19mm T&G F11 Plywood Flooring.
- 2mm Slip Resistant Vinyl Floor Covering, Coved In Wet Areas.
- 2400mm Internal Ceiling Height.
- Pre-finished Plywood Internal Wall & Ceiling Lining, PVC Joiners , Cornice & Corner Moulds.
- Wall & Ceiling Insulation.
- Colorbond 'Panelrib' Profile Horizontal Wall Cladding.
- Zinalume 'Trimdek' Profile Roof Sheeting.
- Colorbond Barge Capping, Gutters & Downpipes.
- Plumbing Waste To Be Harnessed To A Single Connection Point.

Electrical Legend

Icon	Qty	Description
DSB	x(1)	Internal Lockable Distribution Switchboard.
JB	x(1)	Junction Box - Point Of Entry.
⌚	x(3)	Light Switch (Double Pole).
⌚	x(3)	10amp Single GPO (Double Pole).
⌚ WP	x(1)	External 10amp Single GPO (Double Pole).
⌚	x(3)	600mm LED Internal Light Fitting.
⌚	x(3)	Wall Mounted Exhaust Fan.

CLIENT APPROVAL

Signature:

Date:

Rev.	Description	Date	By
A	Issued for Client Review	10/07/24	AW



THIS DRAWING AND DESIGN IS THE SOLE PROPERTY OF TRANSPORTABLE BUILDINGS AUSTRALIA PTY LTD T/AS TRANSBUILD, ABN 45 082 023 354. IT MAY NOT BE REPRODUCED, COPIED WHOLE OR IN PART WITHOUT WRITTEN AUTHORITY.

CLIENT		DATE
		10/07/24
TITLE		SCALE
3.6x2.4m TOILET - FLOOR PLAN		1:50
DESIGN WIND LOAD	DRAWN	CHECKED
C2 (W50C)	AW	
DRAWING NUMBER	REVISION	SHEET SIZE
SQF-4384-01	A	A3