


PRELIMINARY DRAWING

Colour Schedule		
External		
Cladding	-	Surfmist
Roof	-	Zincalume
Capping	-	Surfmist
Gutters	-	Surfmist
Downpipes	-	Surfmist
Doors	-	White
Windows	-	White
Internal		
Vinyl	-	Grey
Walls	-	Grey
Ceiling	-	White
Cabinetry	-	White

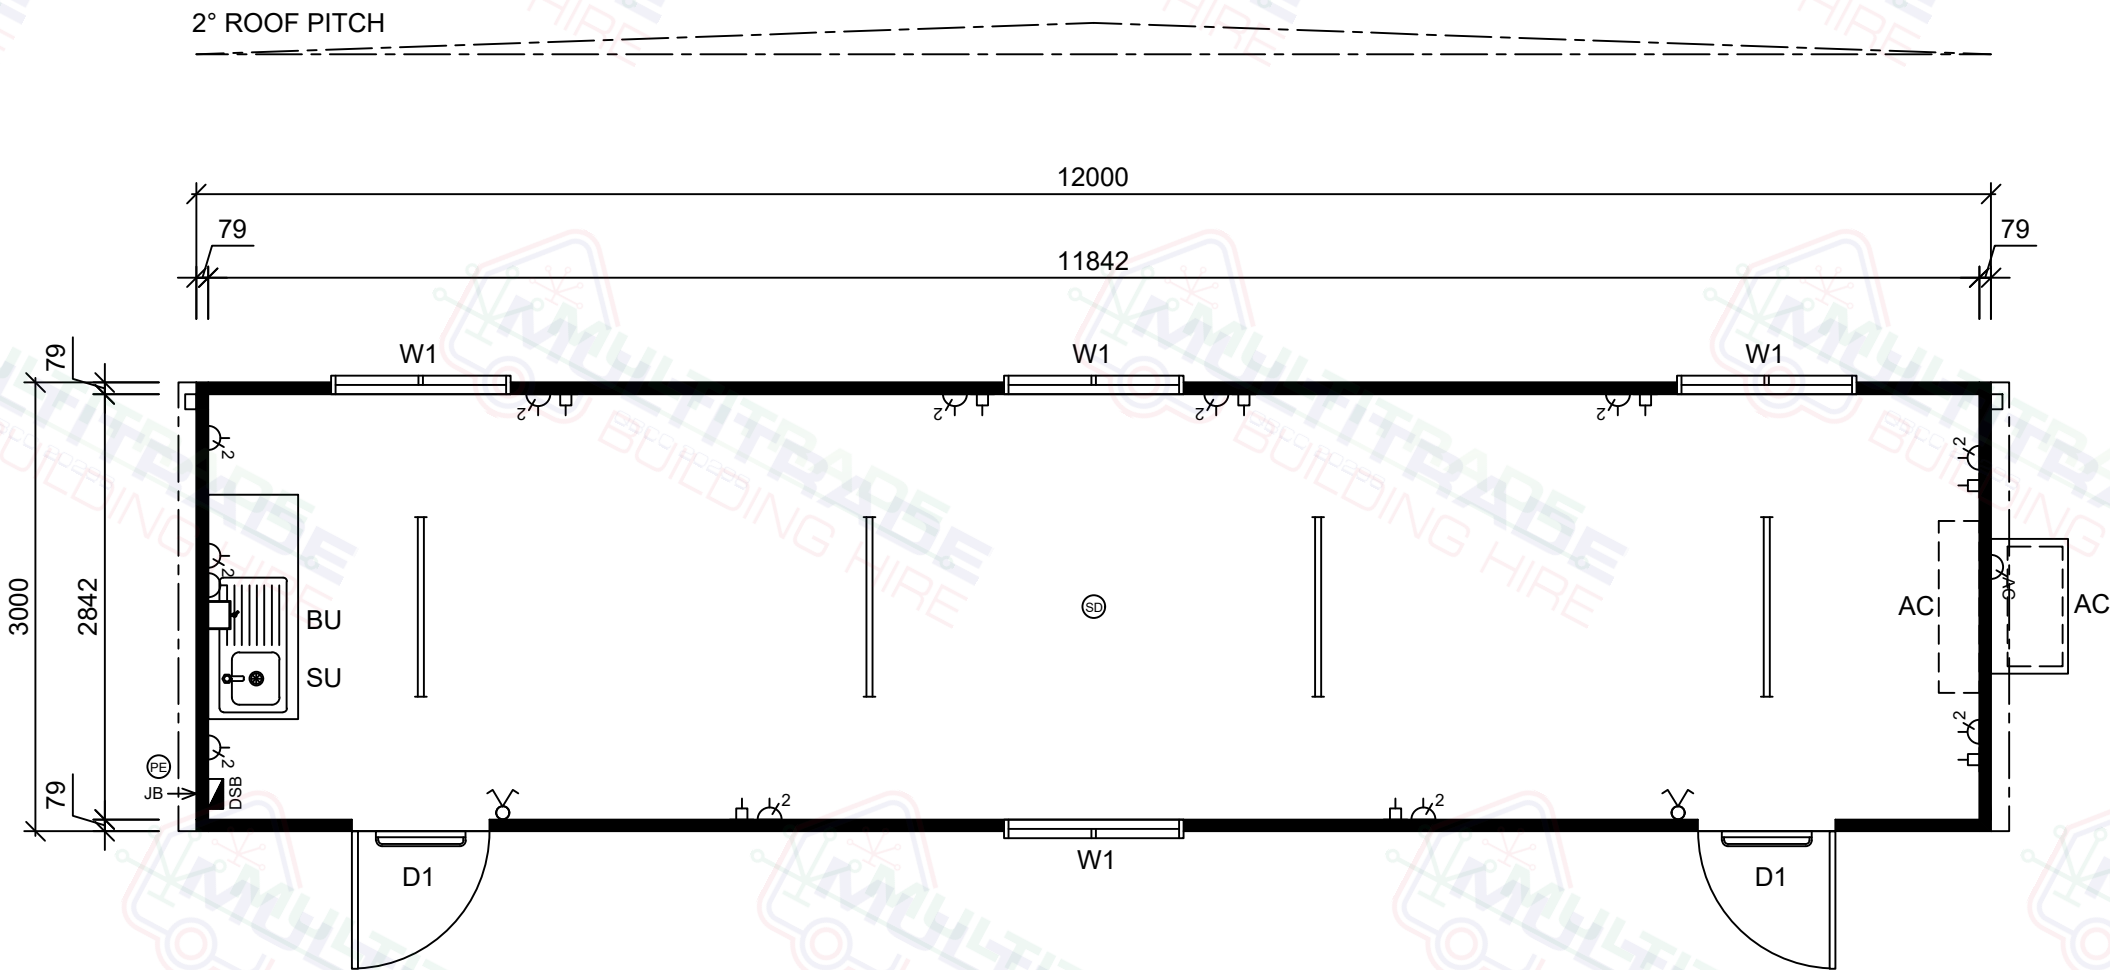

12.0x3.0m Crib Room - Floor Plan

Scale 1:50

Item List

Item	Qty	Description
D1	x(2)	2040x920mm External Metal Clad Door, Glass Viewing Panel, Door Closer, Entrance Lockset.
W1	x(4)	900x1200mm Sliding Glass Window, Flyscreen.
AC	x(1)	7.1kw MHI Split System Reverse Cycle Air Conditioner. <i>*External Unit Mounted On Chassis Extension.</i>
SU	x(1)	1500mm Bench Top With Splashback, Cupboards & Single Drawer Under, Single Bowl/Drainer Sink.
BU	x(1)	3L Boiling Water Unit - Wall Mounted.

Notes

- 75mm Steel Frame Construction.
- 150x75mm PFC Chassis Bearers.
- C10015 Floor Joists @ 600mm Ctrs.
- 19mm T&G F11 Plywood Flooring.
- 2mm Commercial Vinyl Floor Covering.
- 2400mm Internal Ceiling Height.
- Pre-finished Plywood Internal Wall Lining, PVC Joiners, Skirting, Cornice & Corner Moulds.
- Wall & Ceiling Insulation.
- Colorbond 'Panelrib' Profile Horizontal Wall Cladding.
- Colorbond 'Trimdek' Profile Roof Sheeting.
- Colorbond Barge Capping With Gutters & Downpipes.

Electrical Legend

Icon	Qty	Description
	x(1)	Internal Lockable Distribution Switchboard. With Double Pole Main Switch & Double Pole Circuit Breakers & Light Test Point.
	x(1)	Junction Box - Electrical Point Of Entry.
	x(2)	Two Way Light Switch (Double Pole).
	x(1)	10amp Single GPO (Double Pole).
	x(11)	10amp Double GPO (Double Pole).
	x(1)	External Isolator Switch - Split AC.
	x(8)	Draw Wire With Blank Plate.
	x(4)	1200mm LED Internal Light Fitting.
	x(2)	600mm LED External Light Fitting.
	x(1)	Smoke Detector.
	x(1)	PE Cell.



THIS DRAWING AND DESIGN IS THE SOLE PROPERTY OF TRANSPORTABLE BUILDINGS AUSTRALIA PTY LTD T/AS TRANSBUILD, ABN 45 082 023 354. IT MAY NOT BE REPRODUCED, COPIED WHOLE OR IN PART WITHOUT WRITTEN AUTHORITY.

CLIENT APPROVAL	
Signature:	Date:
Rev.	Description
A	Issued for Client Review
Date	15/10/24
By	AW
CLIENT	
DATE	
15/10/24	
TITLE	
12.0x3.0m CRIB ROOM - FLOOR PLAN	
SCALE	
1:50	
DESIGN WIND LOAD	DRAWN
C2 (W50C)	AW
CHECKED	
DRAWING NUMBER	REVISION
SQF-4445-03	A
SHEET SIZE	A3