


PRELIMINARY DRAWING

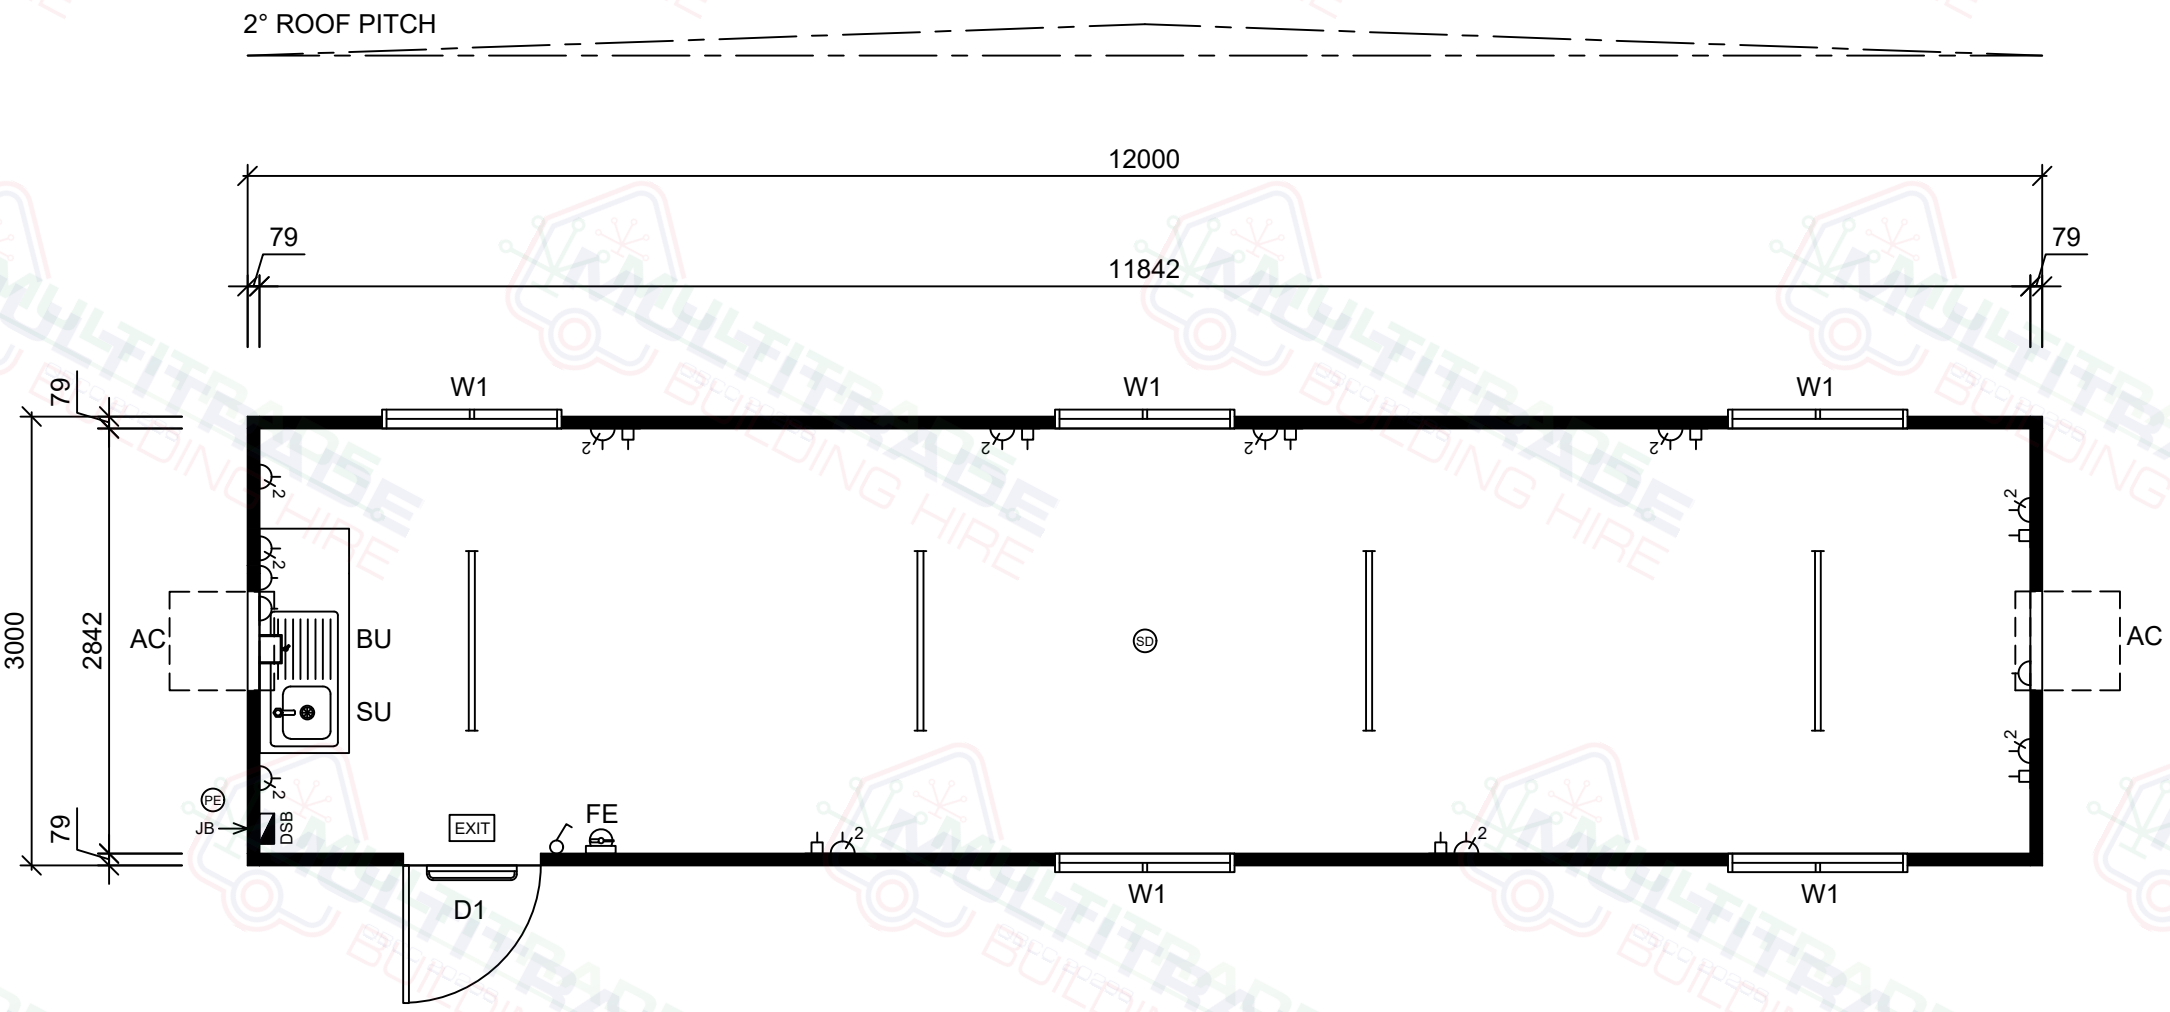

12.0x3.0m Crib Room - Floor Plan

Scale 1:50

Colour Schedule

|          |             |
|----------|-------------|
| External |             |
| Cladding | - Surfmist  |
| Roof     | - Zincalume |
| Capping  | - Surfmist  |
| Doors    | - White     |
| Windows  | - White     |

|           |         |
|-----------|---------|
| Internal  |         |
| Vinyl     | - Grey  |
| Walls     | - Grey  |
| Ceiling   | - White |
| Cabinetry | - White |

CLIENT APPROVAL

Signature: \_\_\_\_\_ Date: \_\_\_\_\_

| Rev. | Description              | Date     | By |
|------|--------------------------|----------|----|
| A    | Issued for Client Review | 18/11/24 | AW |
|      |                          |          |    |
|      |                          |          |    |
|      |                          |          |    |



THIS DRAWING AND DESIGN IS THE SOLE PROPERTY OF TRANSPORTABLE BUILDINGS AUSTRALIA PTY LTD T/AS TRANSBUILD, ABN 45 082 023 354. IT MAY NOT BE REPRODUCED, COPIED WHOLE OR IN PART WITHOUT WRITTEN AUTHORITY.

|        |          |
|--------|----------|
| CLIENT | DATE     |
|        | 18/11/24 |

|                                     |       |
|-------------------------------------|-------|
| TITLE                               | SCALE |
| 12.0x3.0m CRIB ROOM<br>- FLOOR PLAN | 1:50  |

|                  |       |         |
|------------------|-------|---------|
| DESIGN WIND LOAD | DRAWN | CHECKED |
| C2 (W50C)        | AW    |         |

|                |          |            |
|----------------|----------|------------|
| DRAWING NUMBER | REVISION | SHEET SIZE |
| SQF-4467-01    | A        | A3         |

Item List

| Item | Qty  | Description                                                                                                  |
|------|------|---|
| D1   | x(1) | 2040x920mm External Metal Clad Door, Glass Viewing Panel, Door Closer, Entrance Set.                         |
| W1   | x(5) | 900x1200mm Sliding Glass Window, Flyscreen.                                                                  |
| AC   | x(2) | 3.9kw TECO Reverse Cycle Wall Mounted Air Conditioner.                                                       |
| SU   | x(1) | 1500mm Bench Top & Splashback, Cupboards & Single Drawer Under, Single Bowl Single Drainer Sink (Cold Only). |
| BU   | x(1) | 3L Boiling Water Unit - Wall Mounted.                                                                        |
| FE   | x(1) | 4.5kg DCP Fire Extinguisher & Sign.                                                                          |

Notes

- 75mm Steel Frame Construction.
- 150x75mm PFC Chassis Bearers.
- C10015 Floor Joists @ 600mm Ctrs.
- 19mm T&G F11 Plywood Flooring.
- 2mm Commercial Vinyl Floor Covering.
- 2400mm Internal Ceiling Height.
- Pre-finished Plywood Internal Wall & Ceiling Lining, PVC Joiners, Cornice & Corner Moulds.
- Wall & Ceiling Insulation.
- Bracing Plywood To Both 3m End Walls.
- Colorbond 'Panelrib' Profile Horizontal Wall Cladding.
- Zincalume 'Trimdek' Profile Roof Sheeting.
- Colorbond Barge Capping With Stop Ends.

Electrical Legend

| Icon           | Qty   | Description   |
|----------------|-------|---|
| DSB            | x(1)  | Metal Lockable Distribution Board, Double Pole 10kA Rated Main Switch, Double Pole 10kA Rated Breakers With Cirlock Breakers, Light Testing Point & Emergency Light Test Kit. |
| JB             | x(1)  | IP66 Junction Box - Point Of Entry.   |
| LS             | x(1)  | Light Switch (Double Pole).   |
| GPO            | x(3)  | 10amp Single GPO (Double Pole).   |
| GPO            | x(11) | 10amp Double GPO (Double Pole).   |
| Draw Wire      | x(8)  | Draw Wire/Blank Plate.   |
| LED            | x(4)  | 1200mm LED Internal Light Fitting.   |
| LED            | x(1)  | 600mm LED External Light Fitting.   |
| EXIT           | x(1)  | Emergency Exit Light.   |
| Smoke Detector | x(1)  | Smoke Detector.   |
| PE Cell        | x(1)  | PE Cell.   |