


PRELIMINARY DRAWING

Colour Schedule

External		
Cladding	-	Surfmist
Roof	-	Zincalume
Capping	-	Surfmist
Doors	-	White
Windows	-	White

Internal		
Vinyl (R10)	-	Grey
Walls	-	Grey
Ceiling	-	White

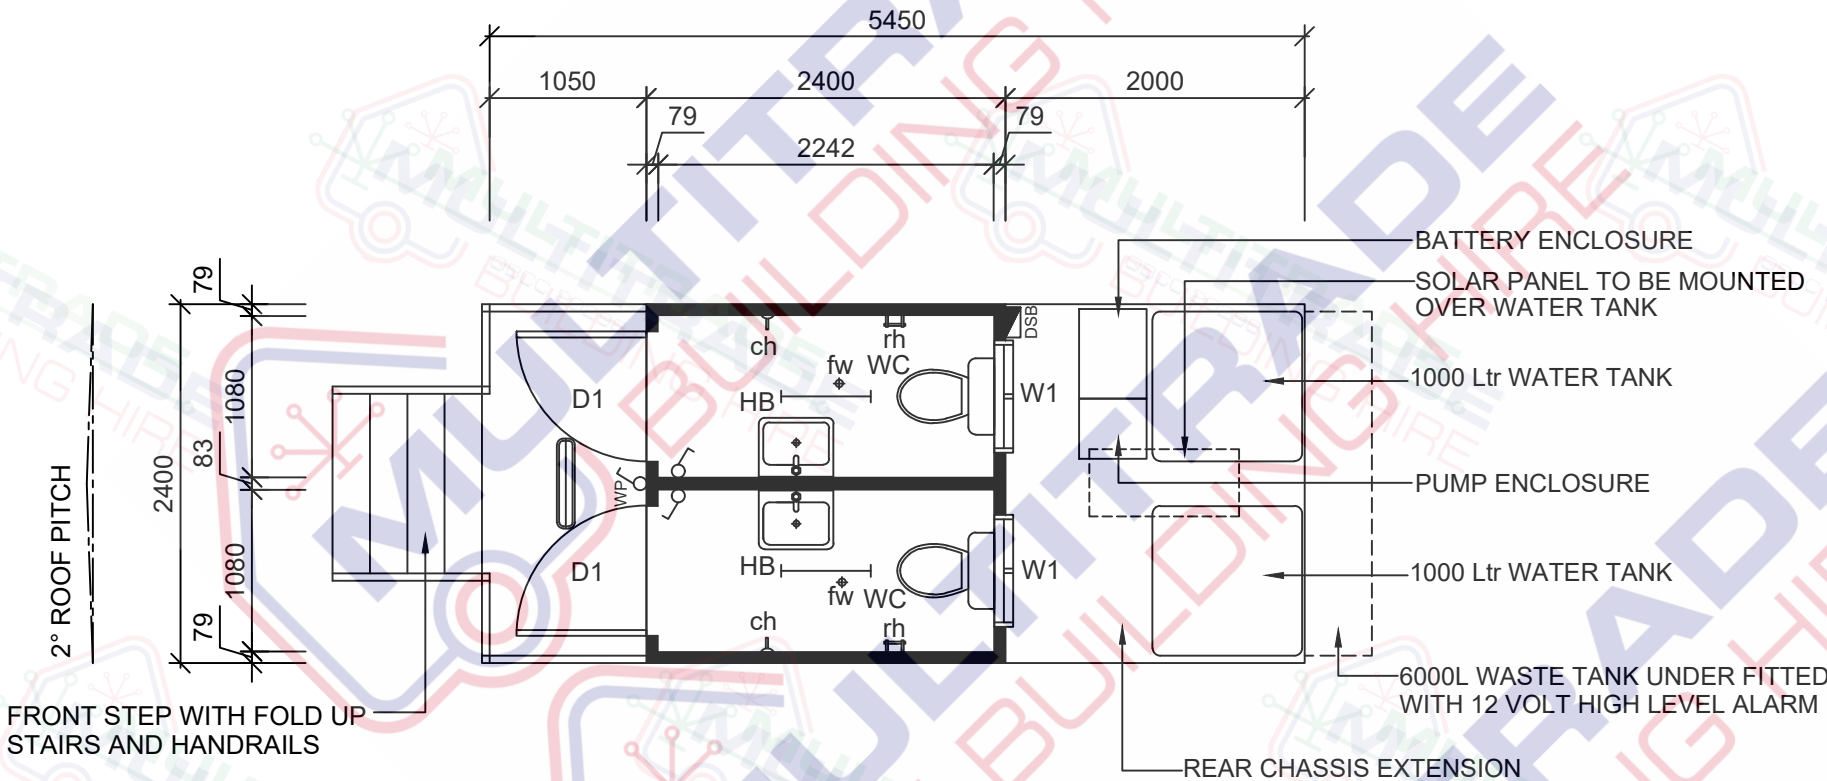

5.45x2.4m Solar Toilet / 6000L Waste Tank - Floor Plan

Scale 1:50

Item List

Item	Qty	Description
D1	x(2)	2040x820mm External Metal Clad Door, Door Vent, Privacy Set, Door Closer, Toilet Sign.
W1	x(2)	300x750mm Obscure Sliding Glass Window, Flyscreen.
WC	x(2)	Toilet Pan With Dual Flush Cistern - 'P' Trap
HB	x(2)	Stainless Steel Hand Basin, Splashback - Spring Tap (Cold), Mirror Over (Note: Basin Waste - 'P' Trap Through Rear Wall).
rh	x(2)	Roll Holder.
ch	x(2)	Coat Hook.
fw	x(2)	Floor Waste.

Notes

- 75mm Steel Frame Construction.
- 150x75mm Bearers
- 50x50x2.0mm SHS Floor Joists @ 600mm Ctrs.
- 19mm T&G F11 Plywood Flooring.
- 2mm Commercial R10 Slip Resistant Vinyl, Coved In Wet Areas.
- 2155mm Internal Ceiling Height.
- Pre-finished Plywood Internal Wall & Ceiling Linings, PVC Joiners, Cornice & Corner Moulds.
- Wall & Ceiling Insulation.
- Colorbond 'Panelrib' Profile Horizontal Wall Cladding.
- Zincalume 'Trimdek' Profile Roof Sheeting.
- Colorbond Barge Capping With Stop Ends.
- Plumbing Waste Harnessed Into 6000L Waste Tank Under Building.

Electrical Legend

Icon	Qty	Description
DSB	x(1)	External Lockable Switchboard, Solar Controller & Circuit Breakers.
WPB	x(2)	Push Button Timer Light Switch
	x(1)	External Push Button Timer Light Switch
	x(2)	12 Volt LED Internal Light Fitting
	x(1)	12 Volt LED External Light Fitting

CLIENT APPROVAL

Signature:

Date:

Rev.	Description	Date	By
A	Issued For Client Review	27/02/25	BW



THIS DRAWING AND DESIGN IS THE SOLE PROPERTY OF JABEGIL PTY LTD T/A MULTITRADE BUILDING HIRE A.B.N. 36 010 138 600 IT MAY NOT BE REPRODUCED, COPIED WHOLE OR IN PART WITHOUT WRITTEN AUTHORITY.

CLIENT		DATE
		27/02/25
TITLE		SCALE
5.45x2.4m TOILET / 6000L TANK - FLOOR PLAN		1:50
DESIGN WIND LOAD	DRAWN	CHECKED
C2 (W50C)	BW	
DRAWING NUMBER	REVISION	SHEET SIZE
SQF-4525-01	A	A3